


Free Strengthen



Studio 44
2020310780 Jeong Mi Joo

Site Analysis

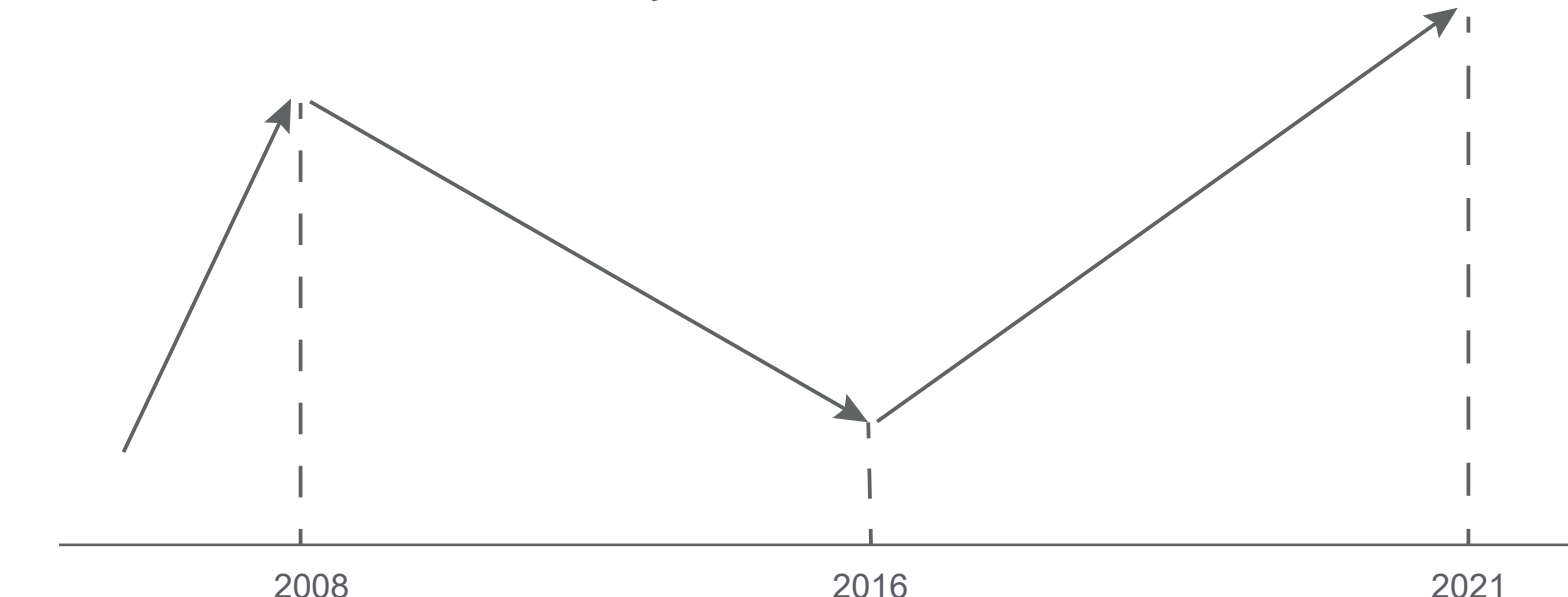

Numbers of game company in Teheran-ro




Game companies are concentrated, so they can enjoy the benefits of the accumulation complex




Easy to link with Seongsu and Gwacheon and Anyang areas in Seoul, where IT content companies are recently gathering


Program

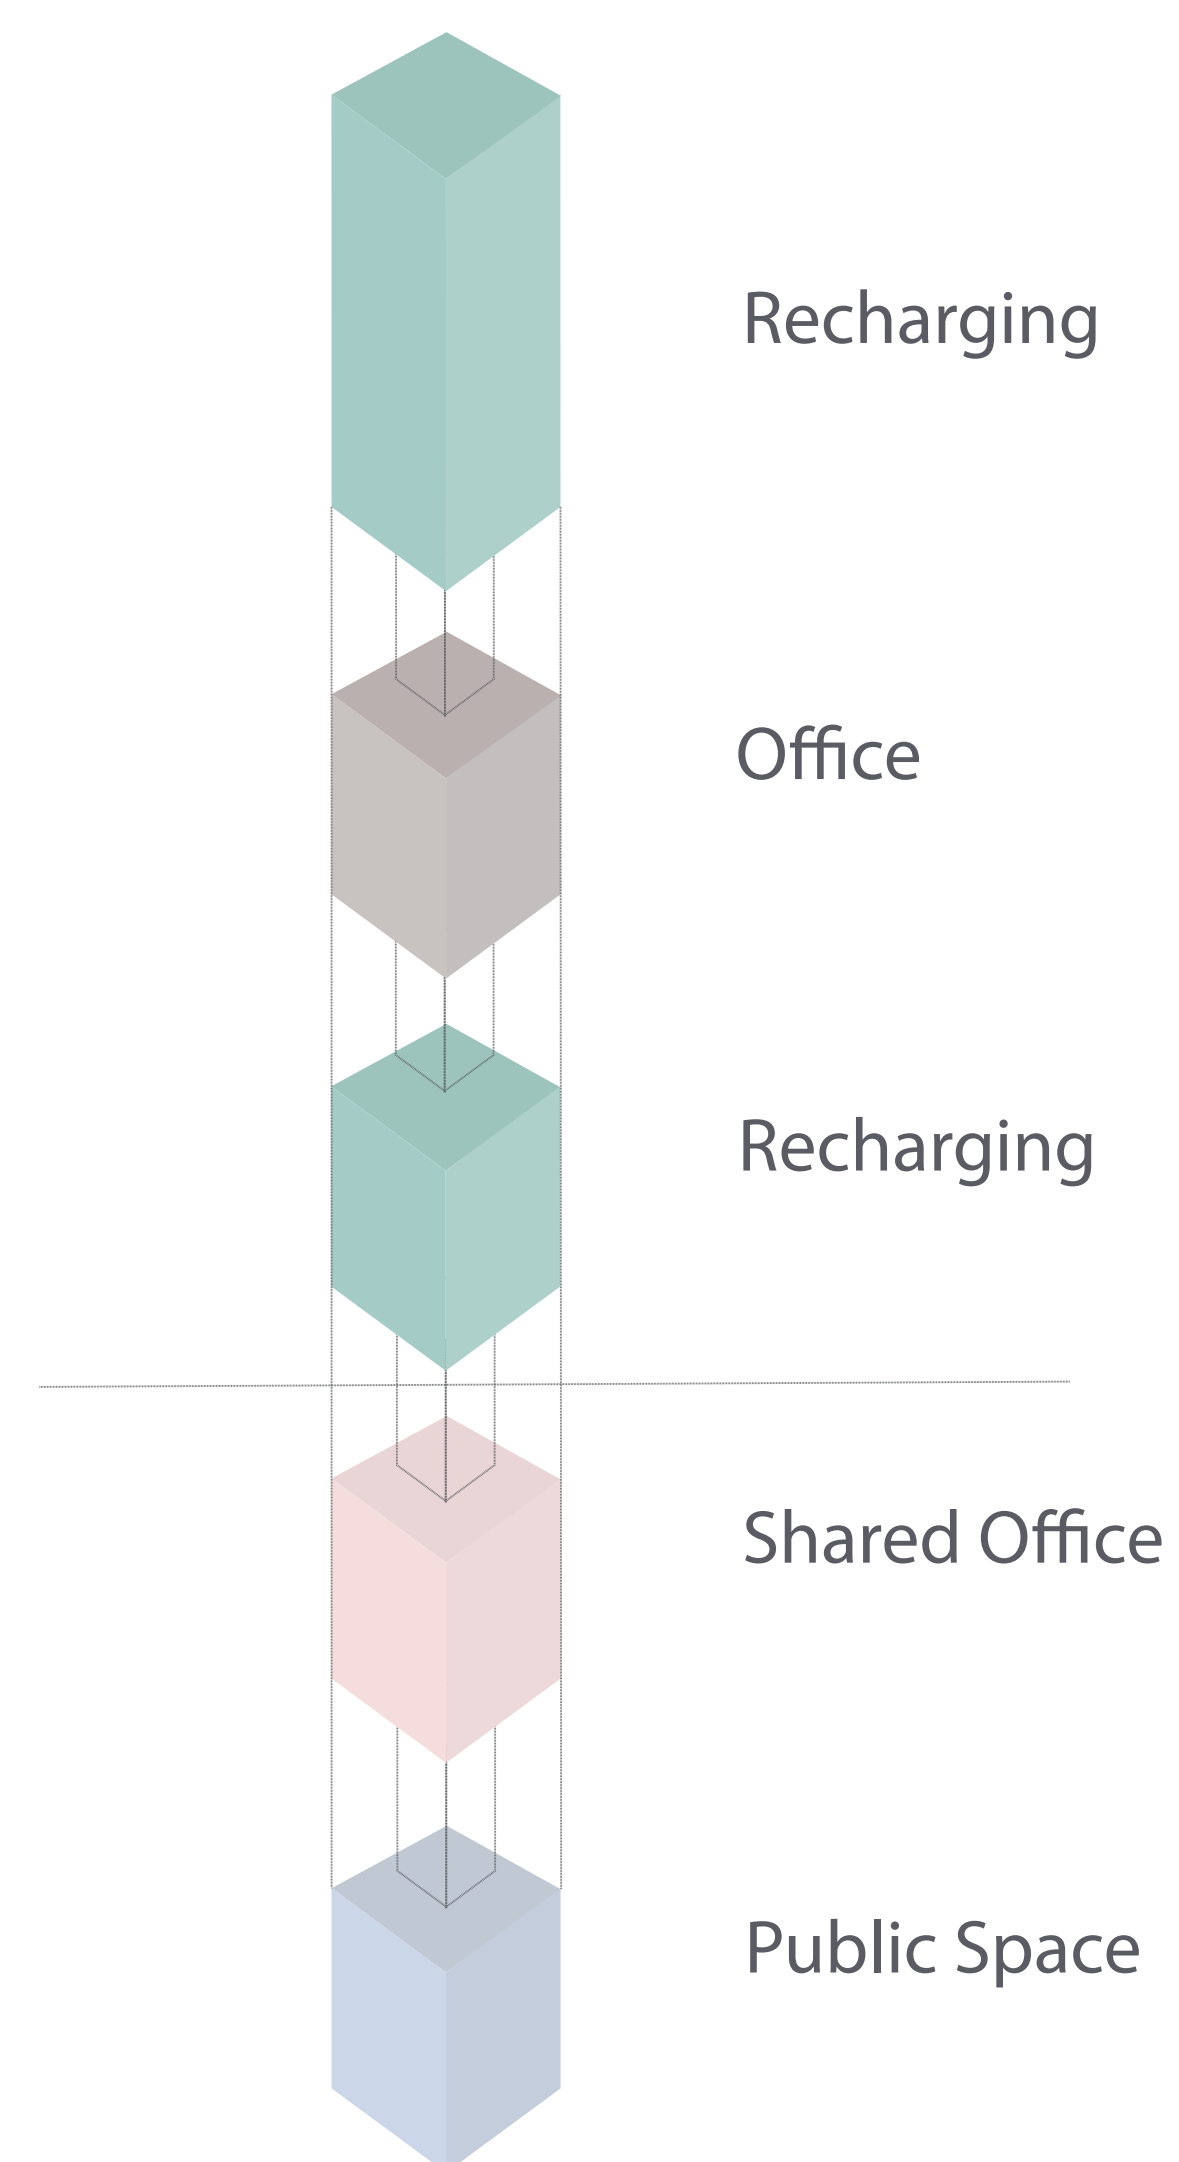


Concept

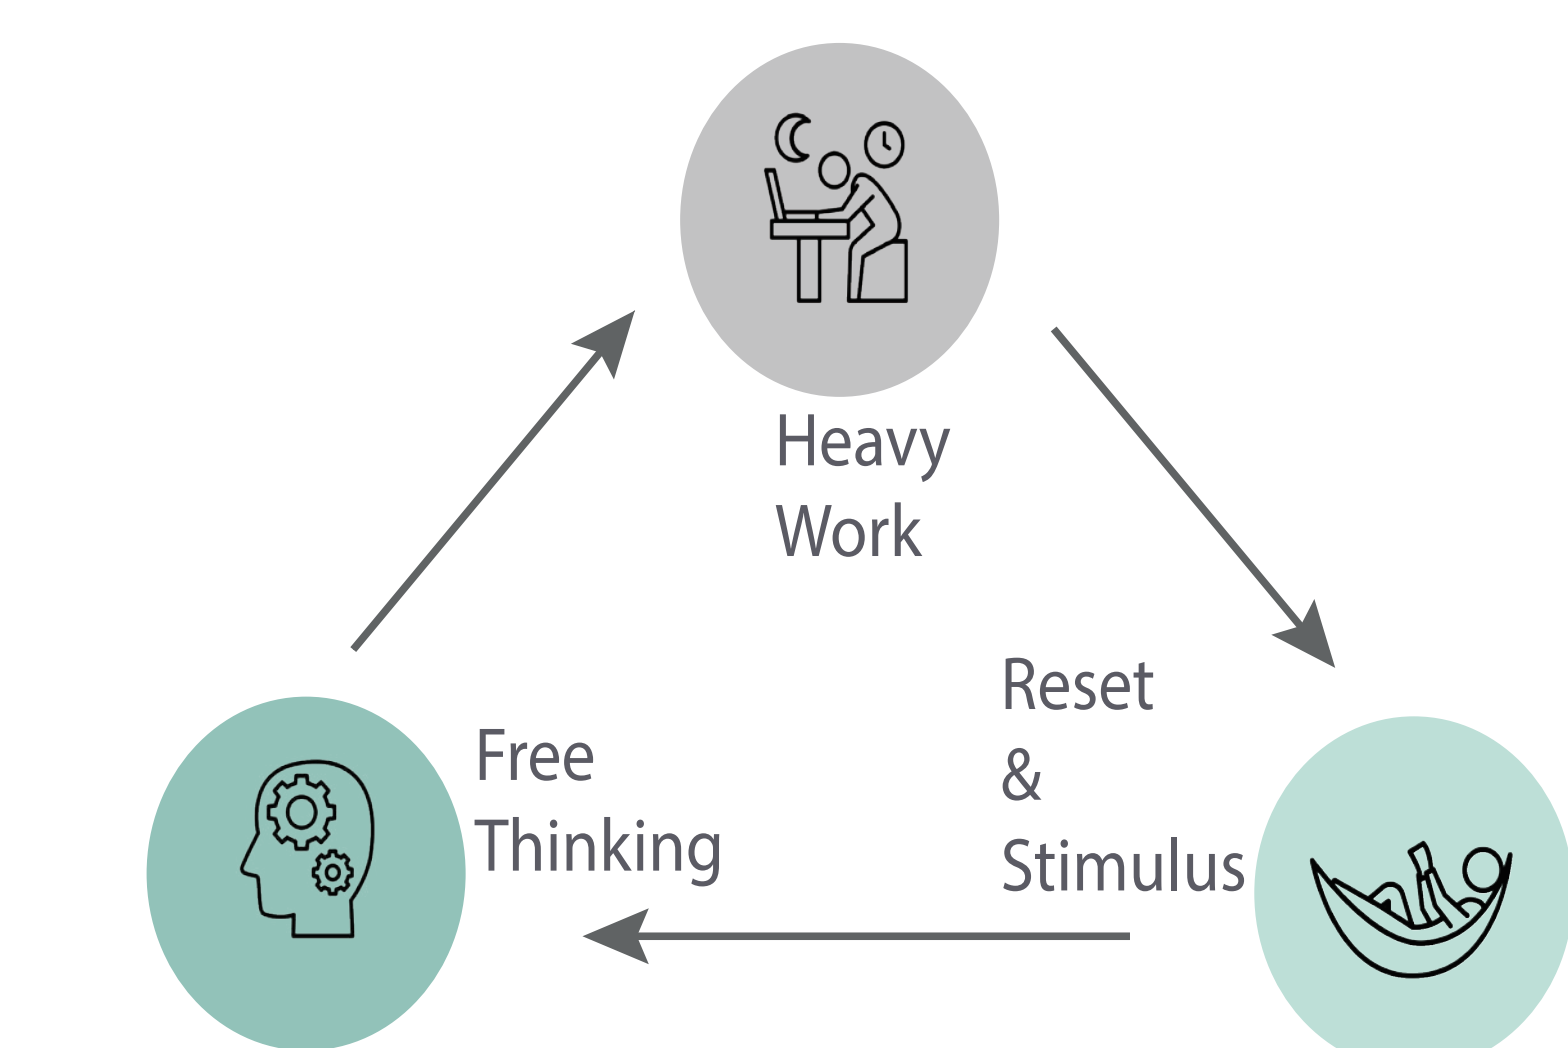


Site Plan

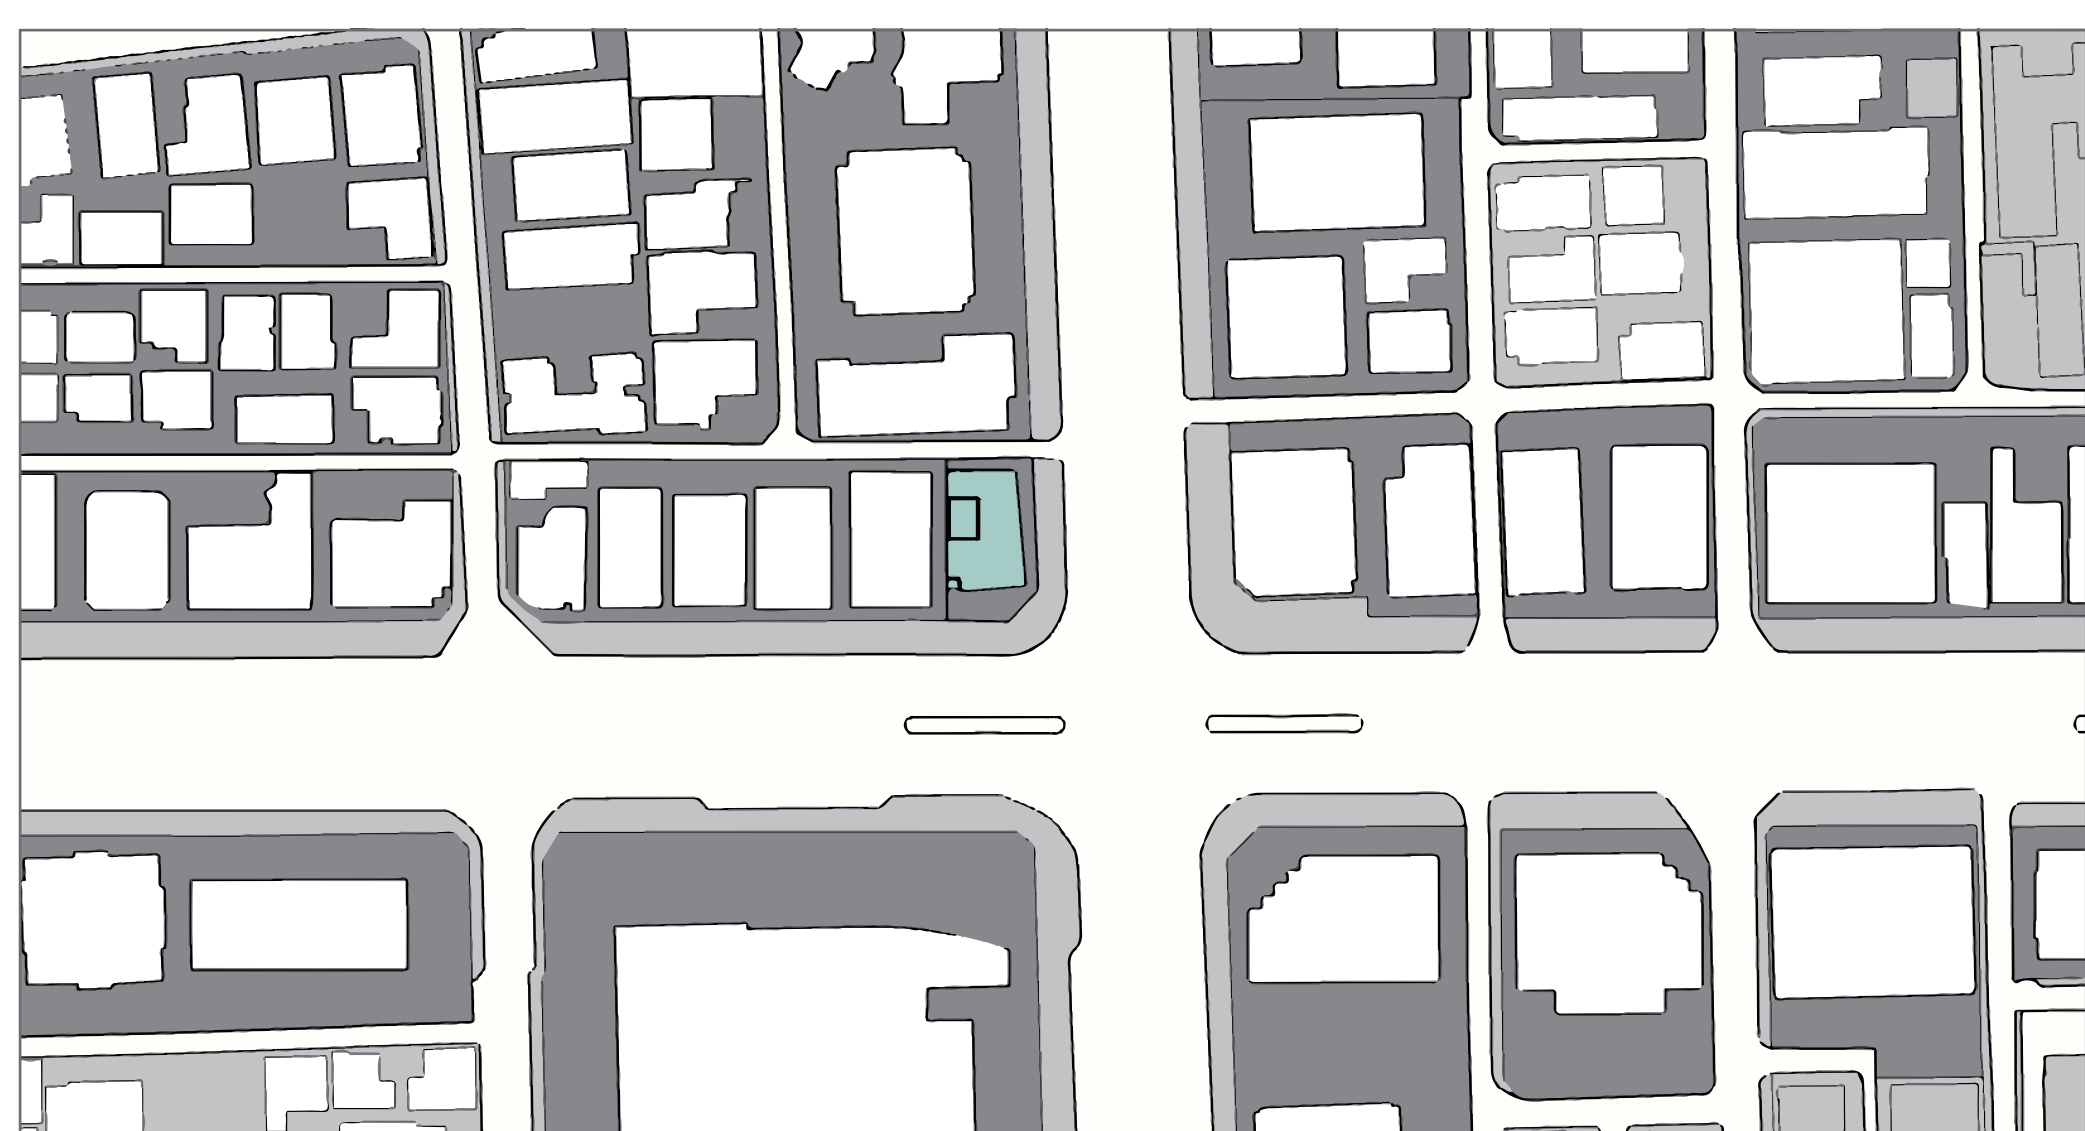


Plan

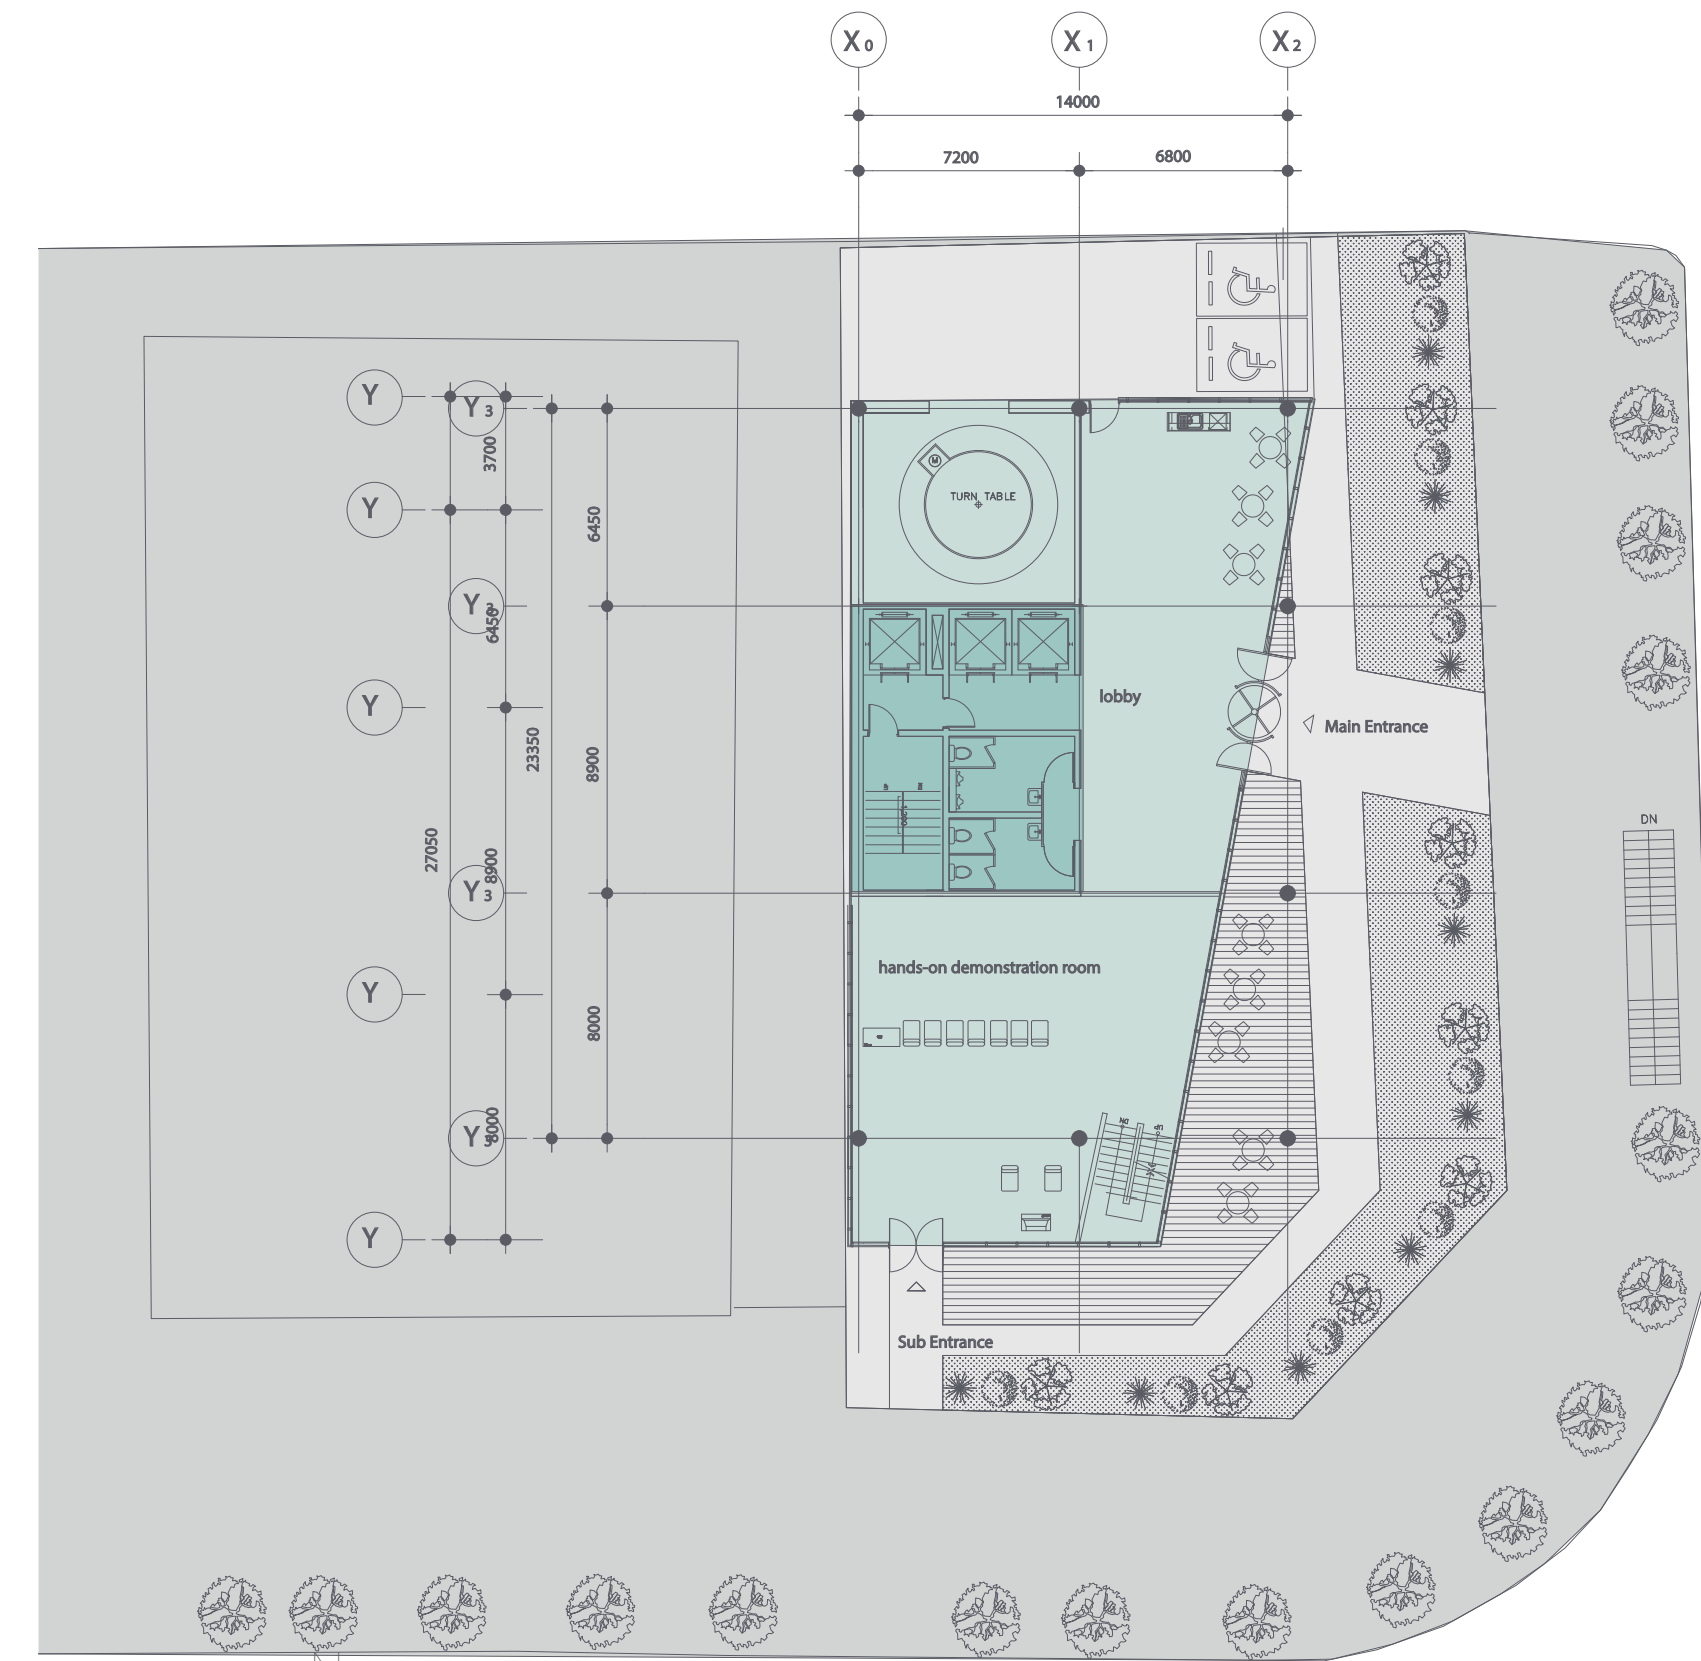


GROUND FLOOR PLAN
SCALE 1/300

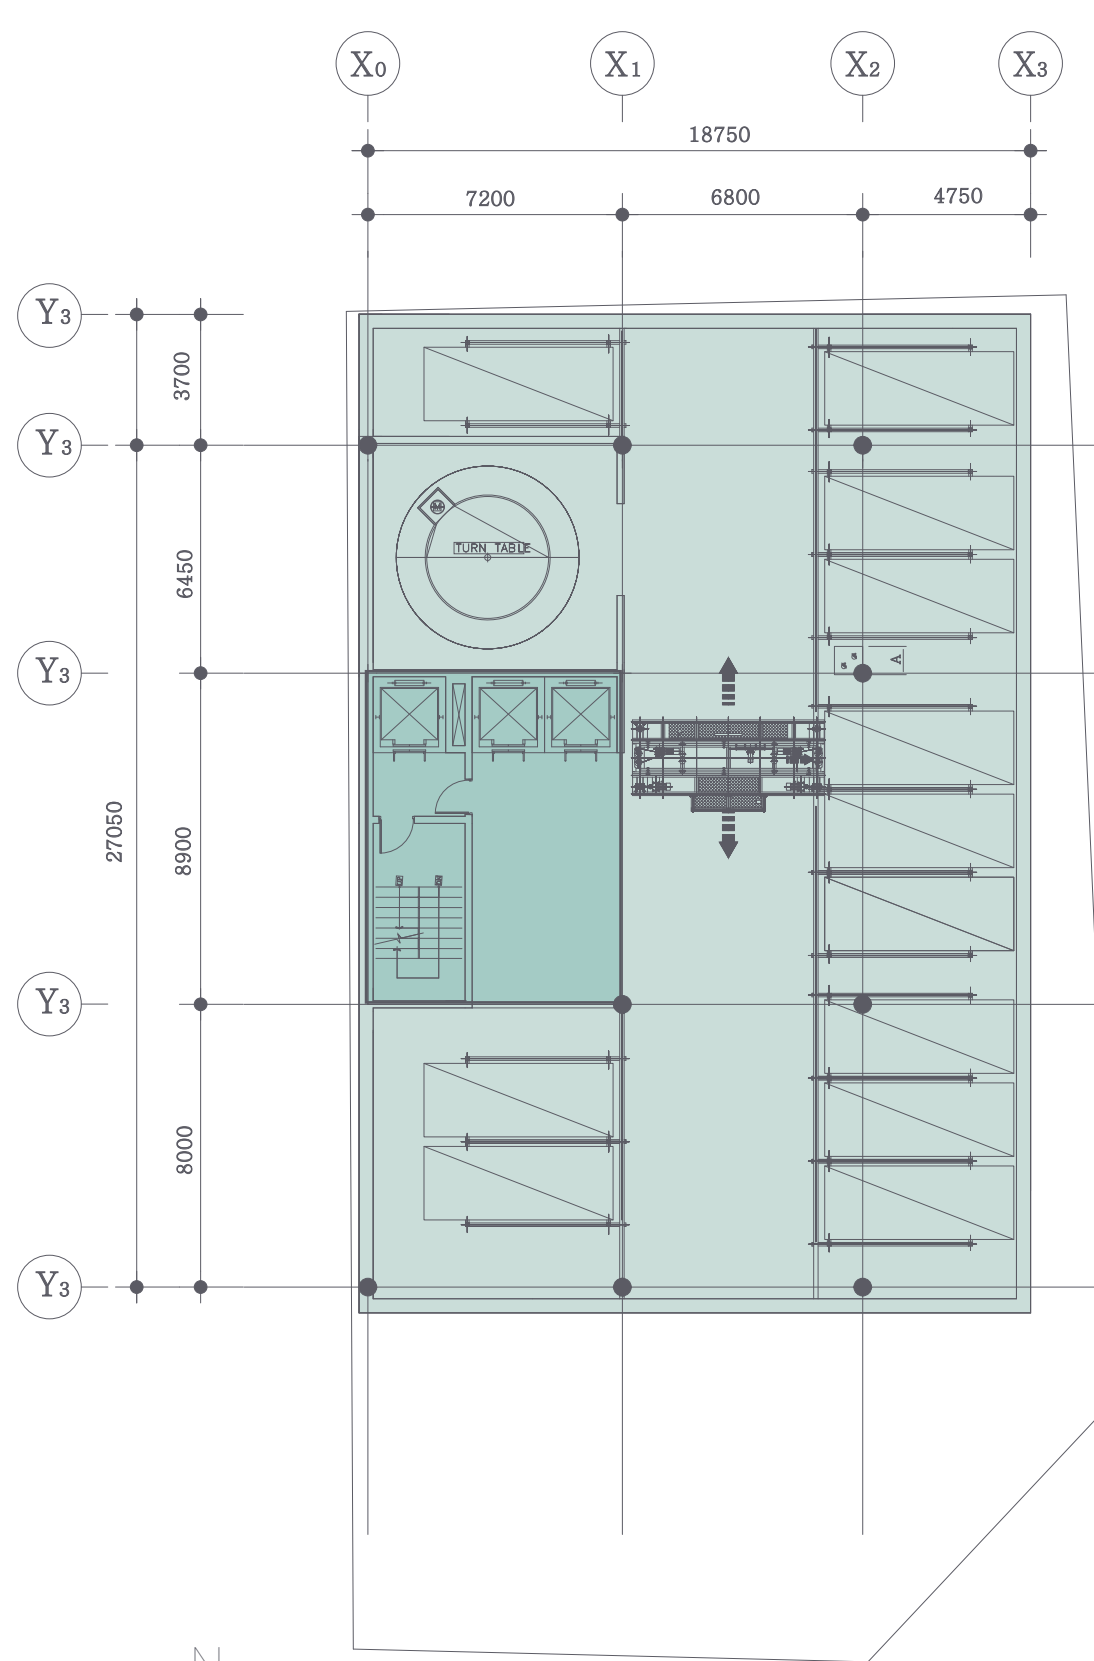


PARKING PLAN
SCALE 1/300

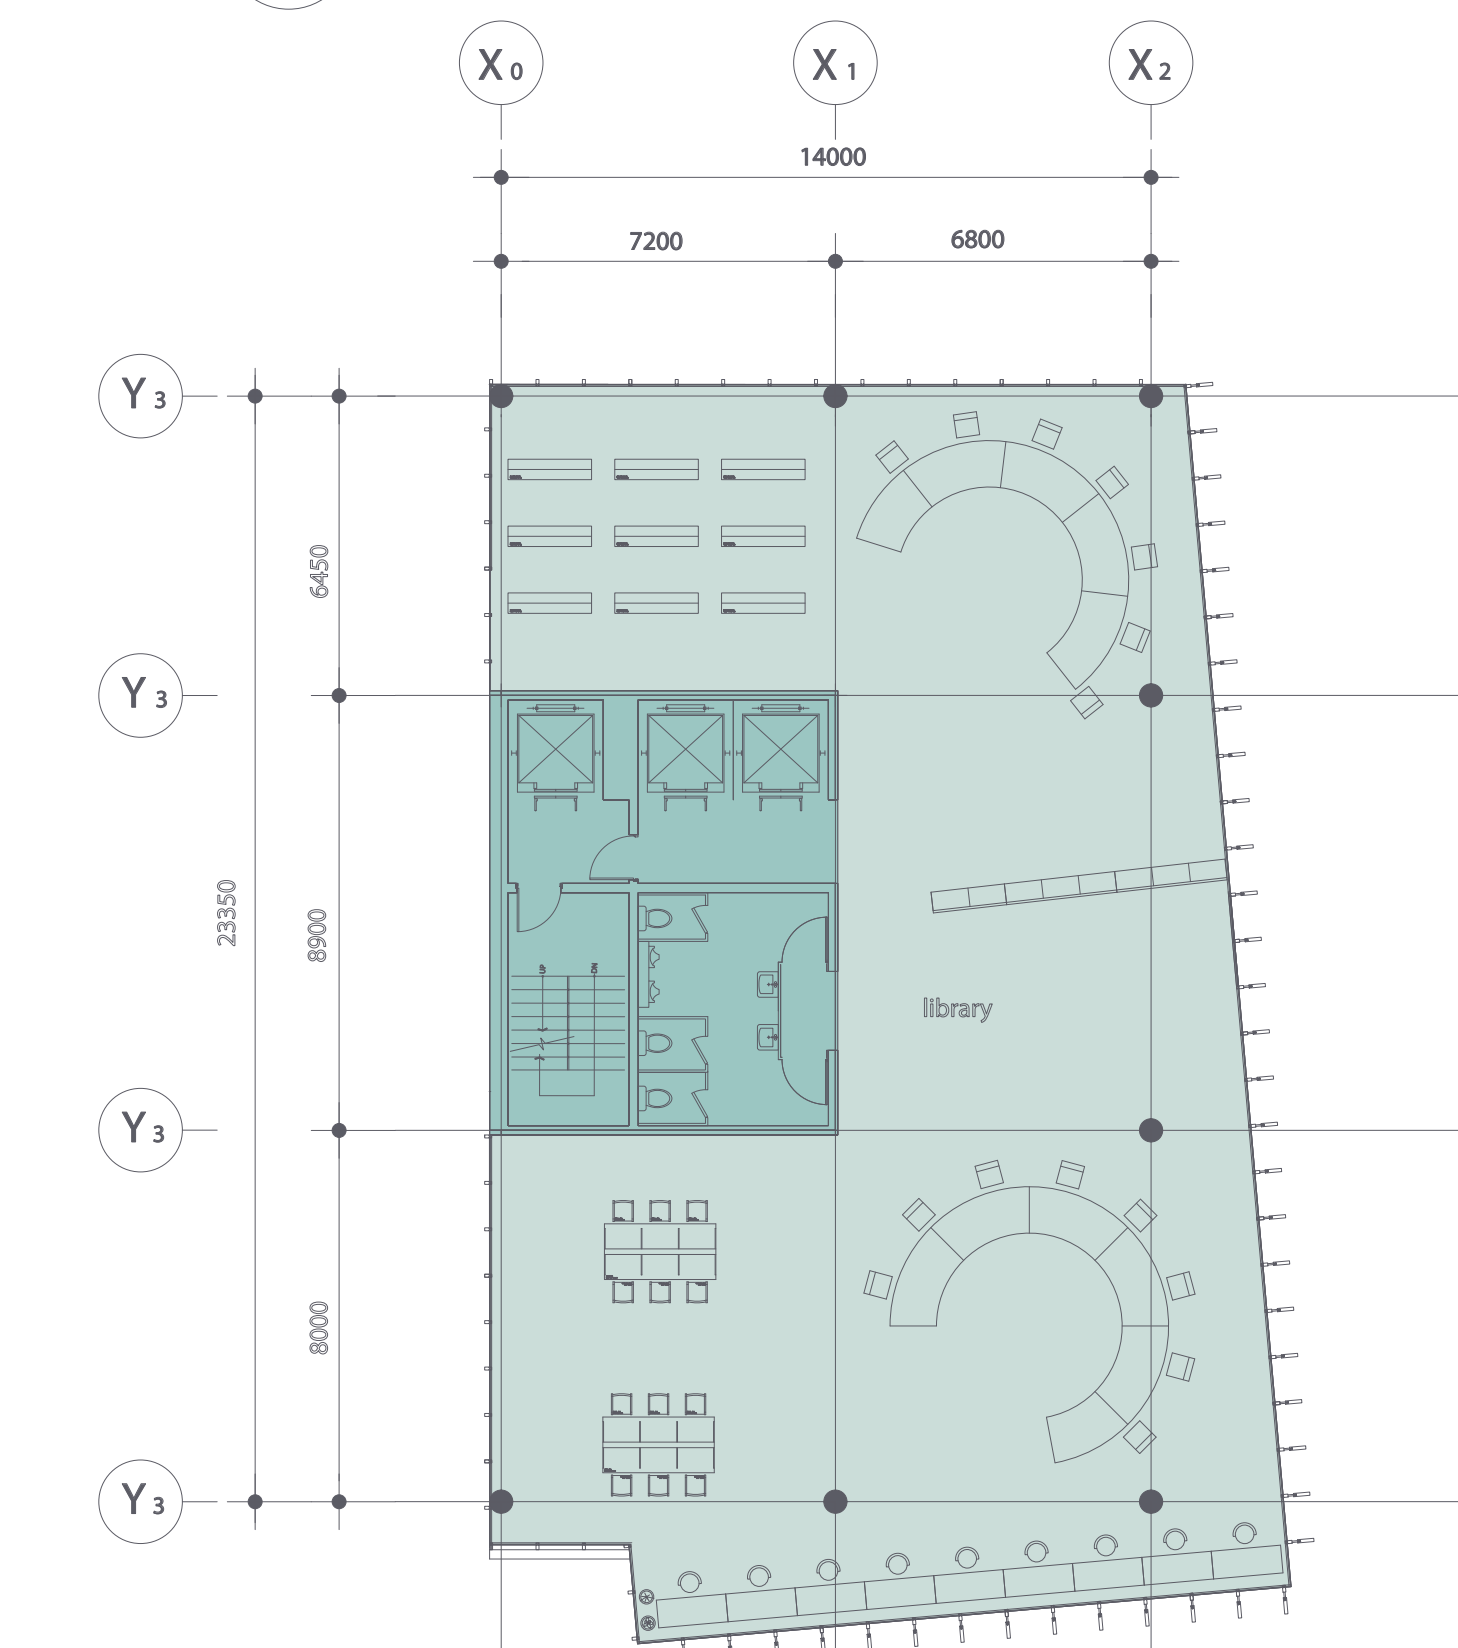


RECHARGING FLOOR PLAN
SCALE 1/300

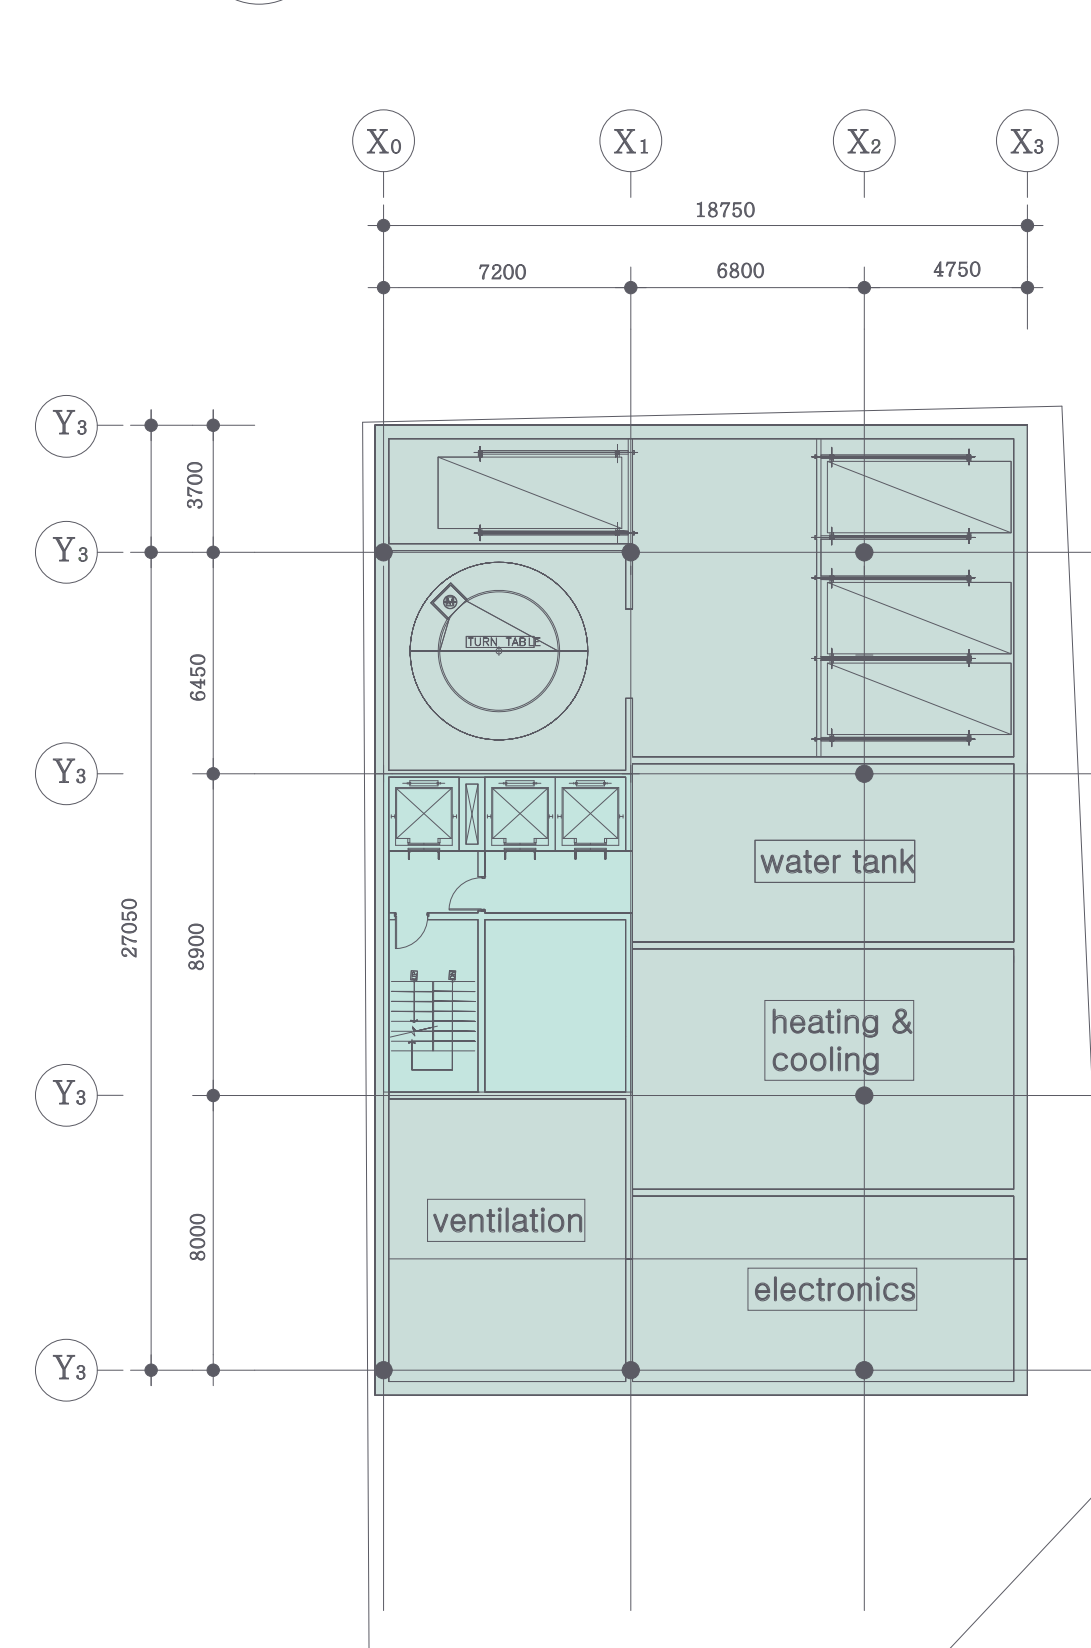

B1 FLOOR PLAN
SCALE 1/300

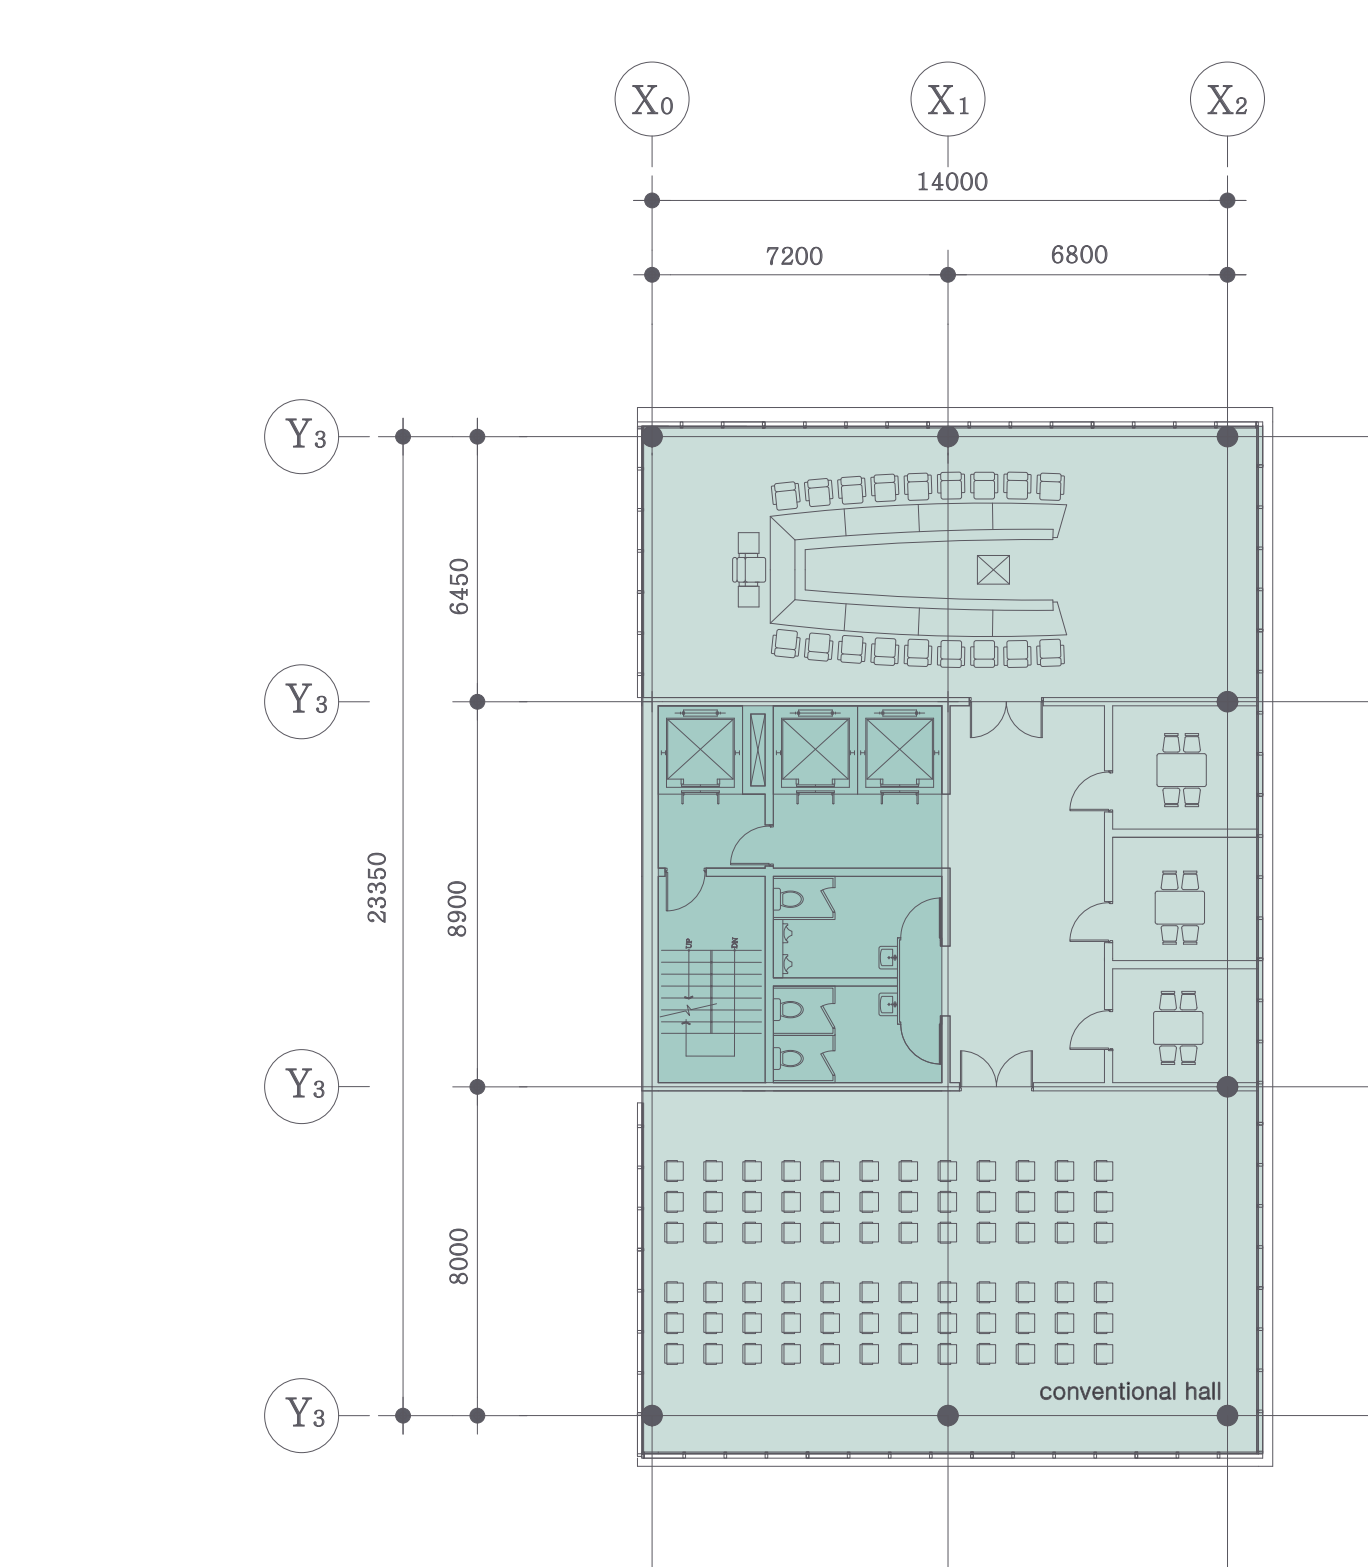


SHARED SPACE PLAN
SCALE 1/300


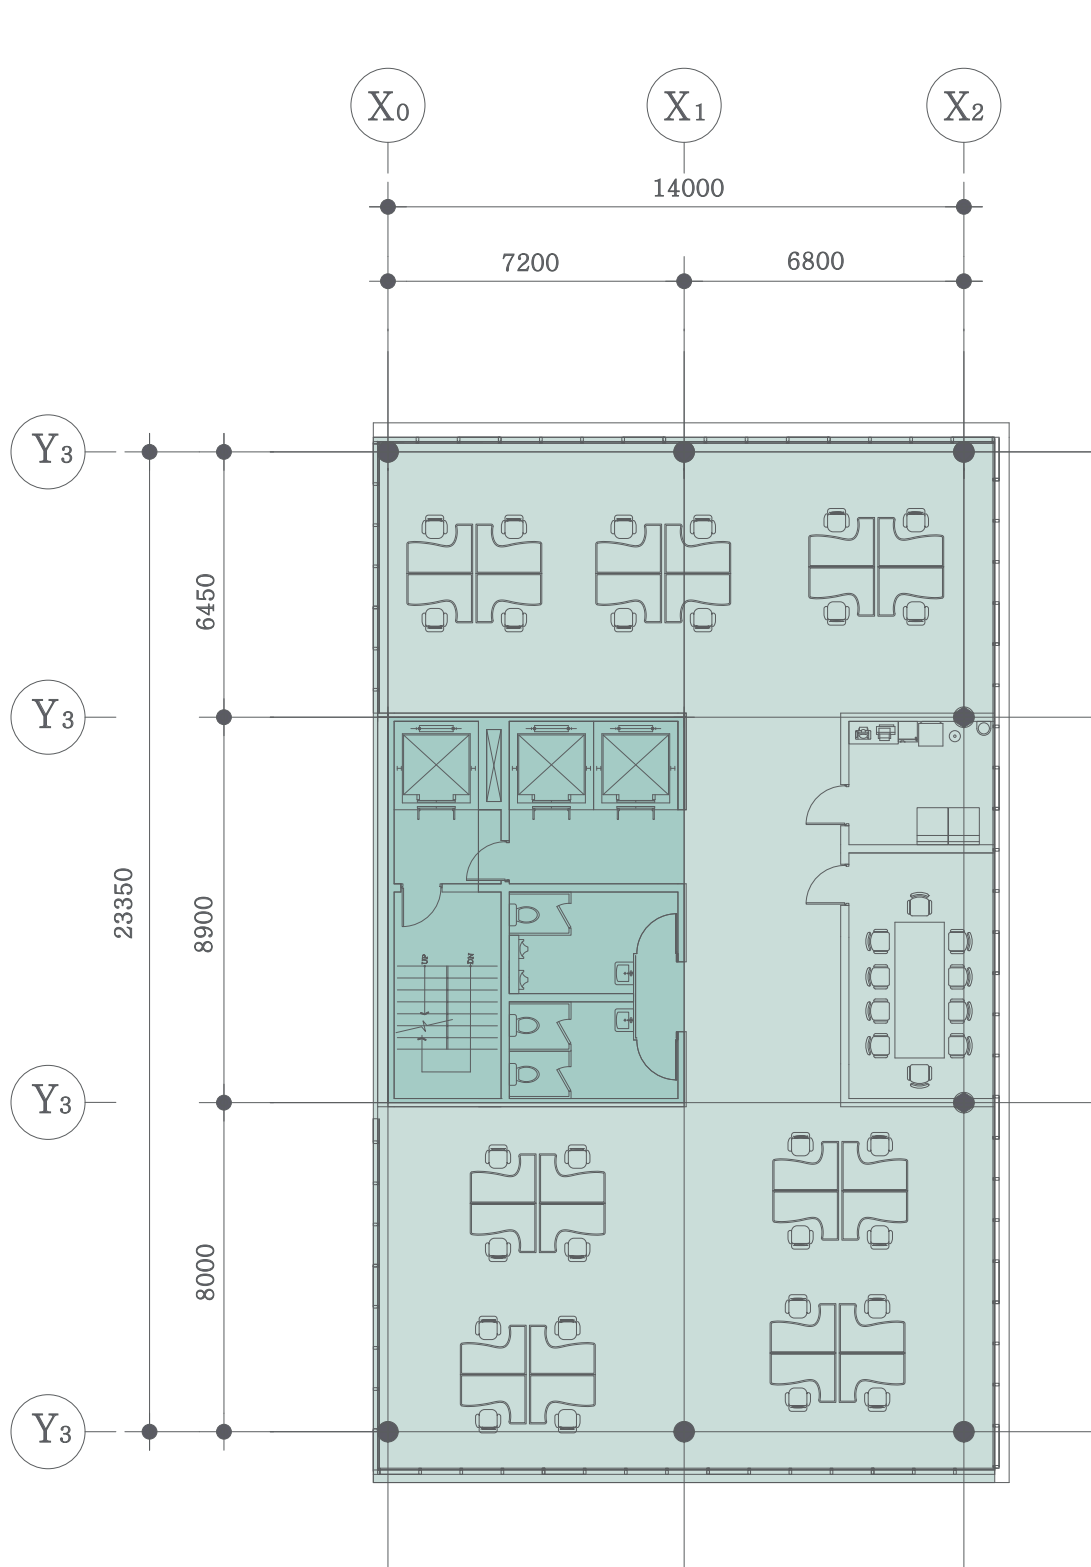




TYPICAL OFFICE PLAN
SCALE 1/300

Section

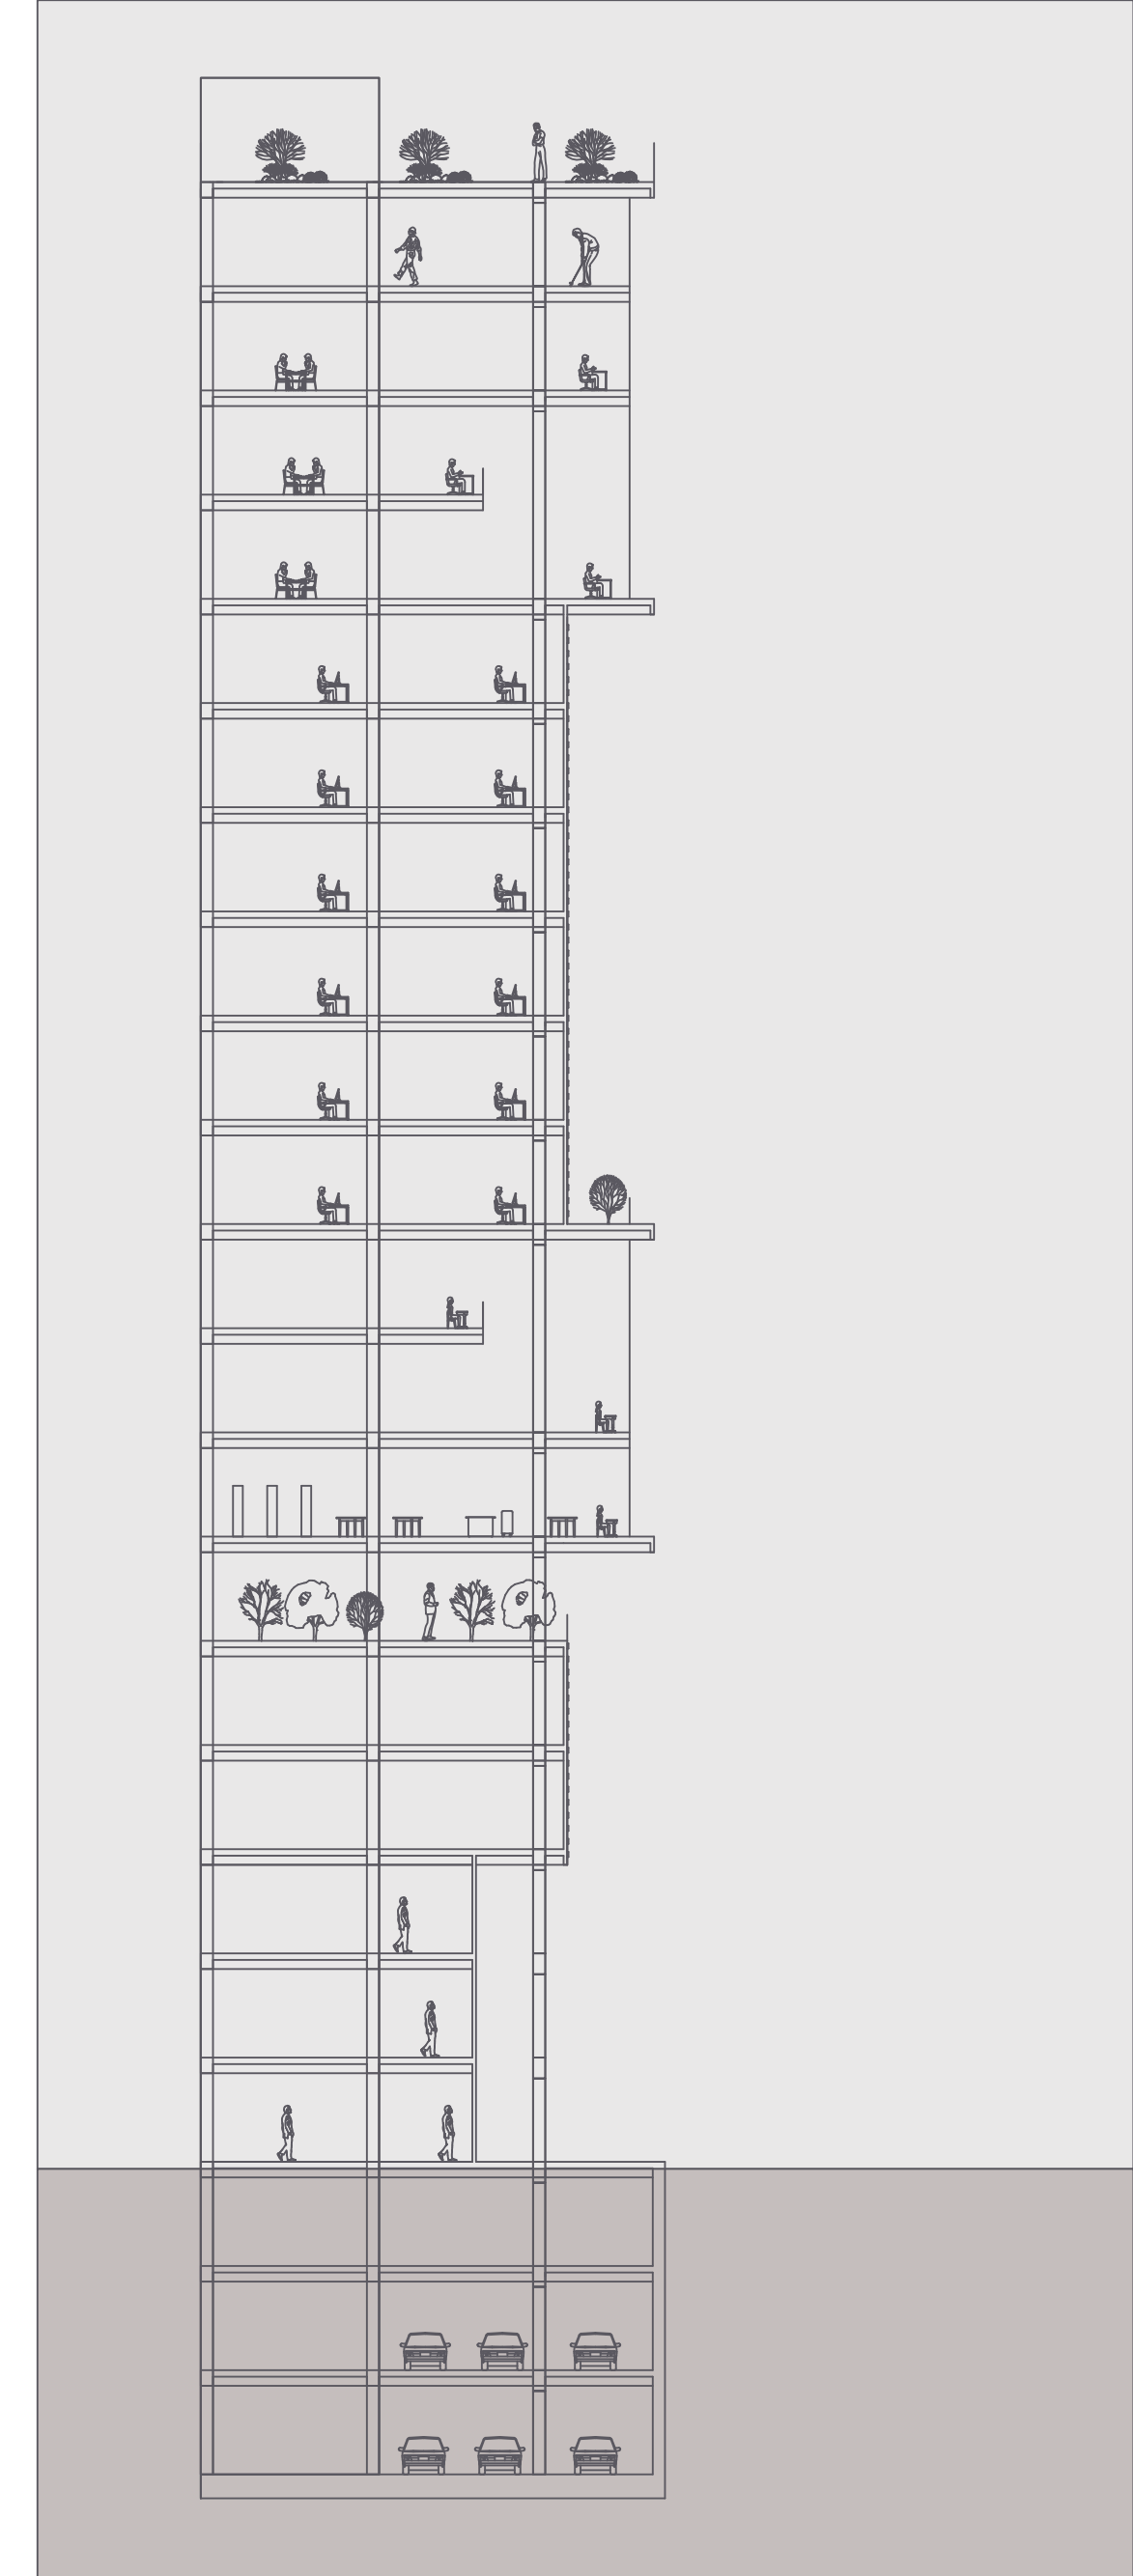


Ceiling Plan

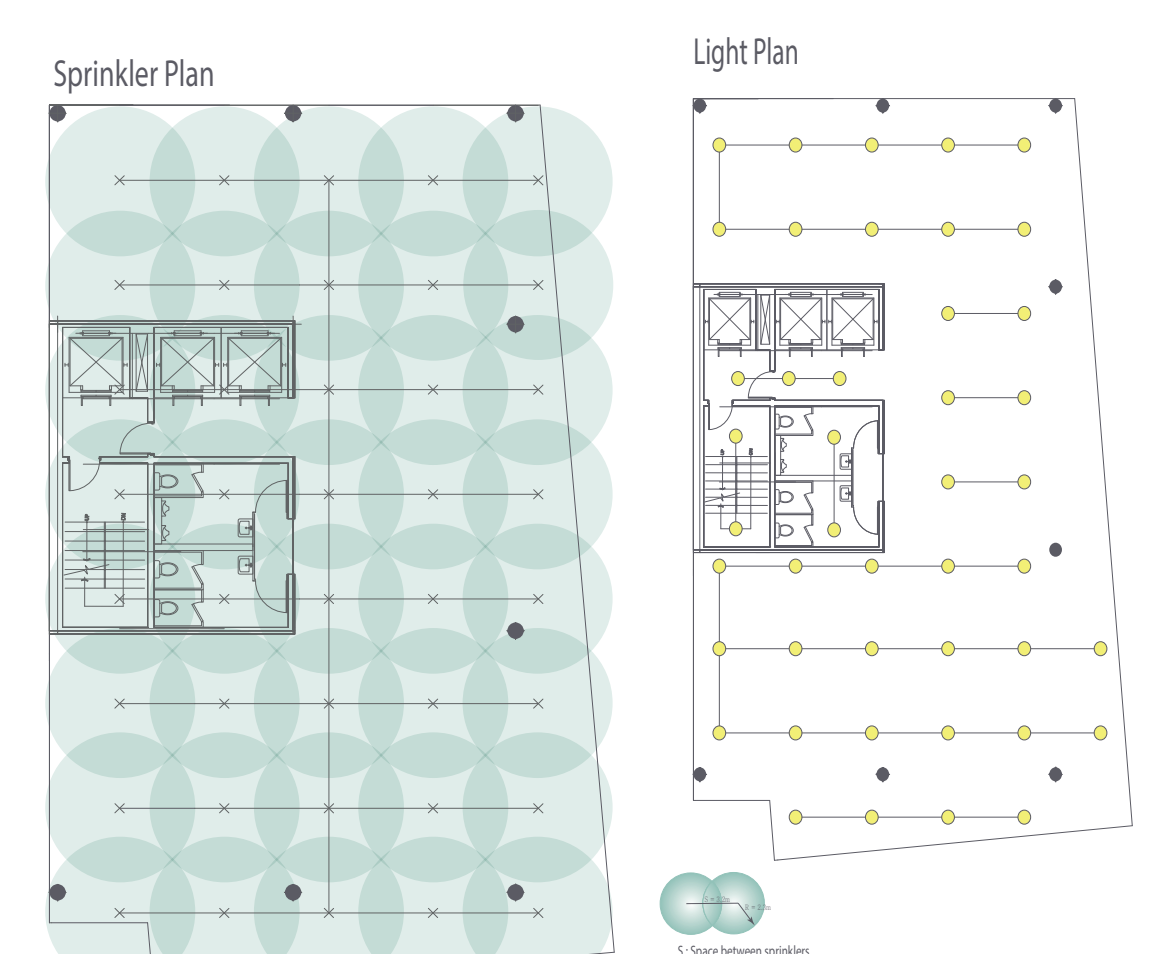
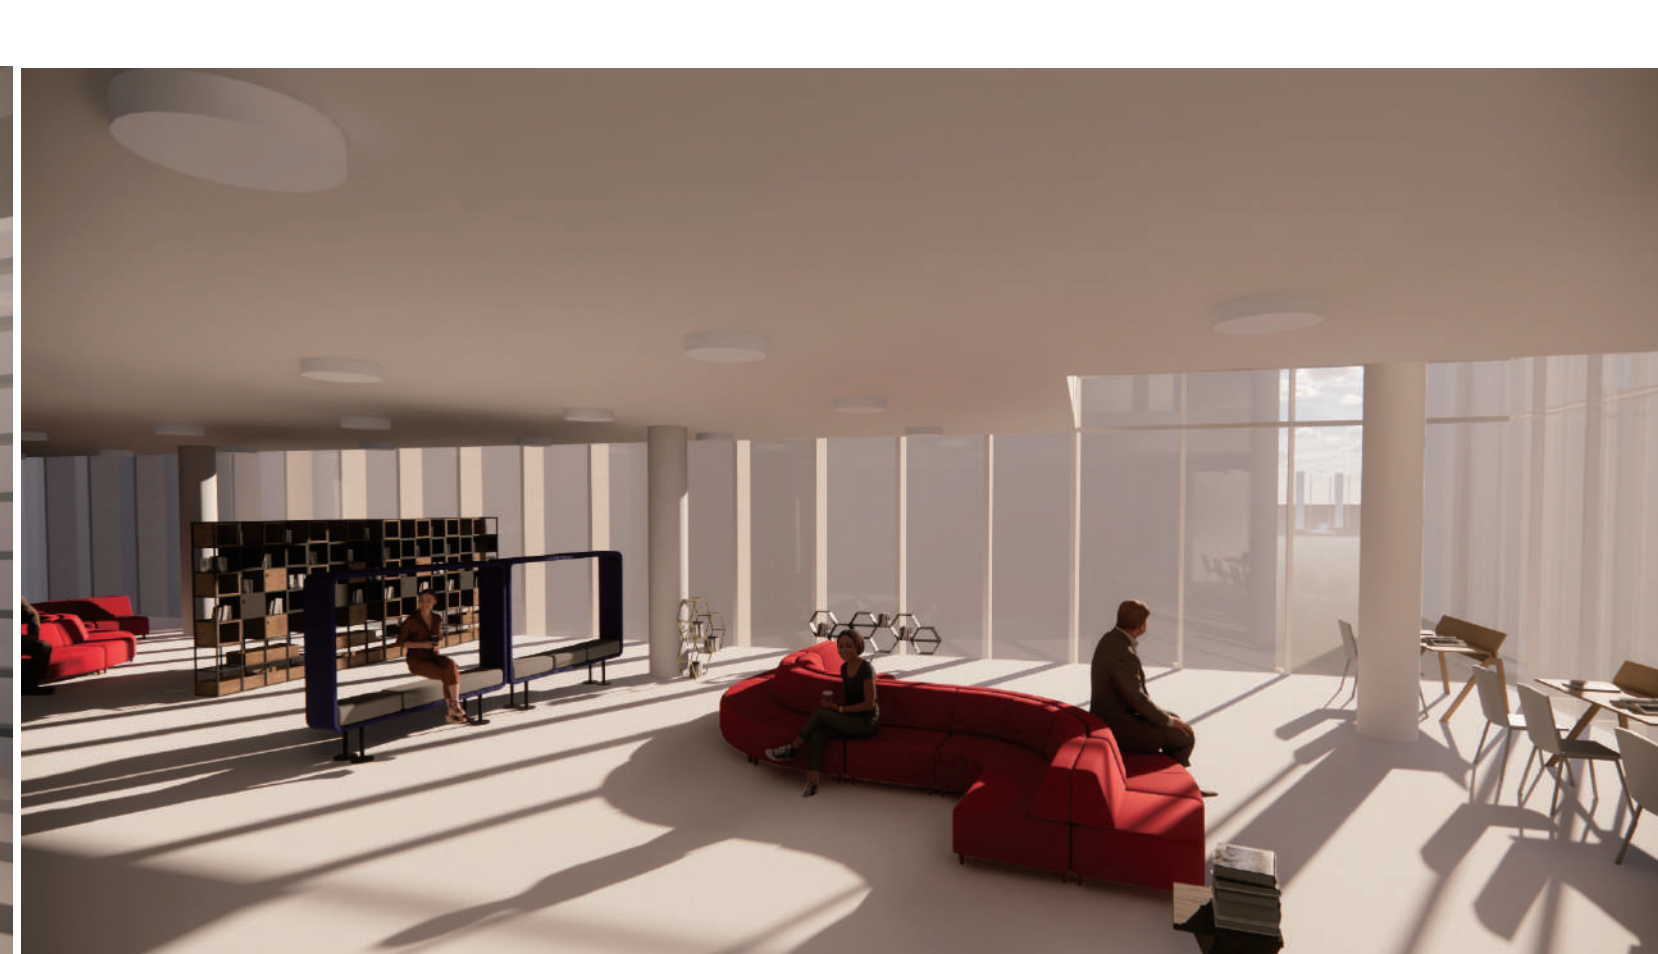


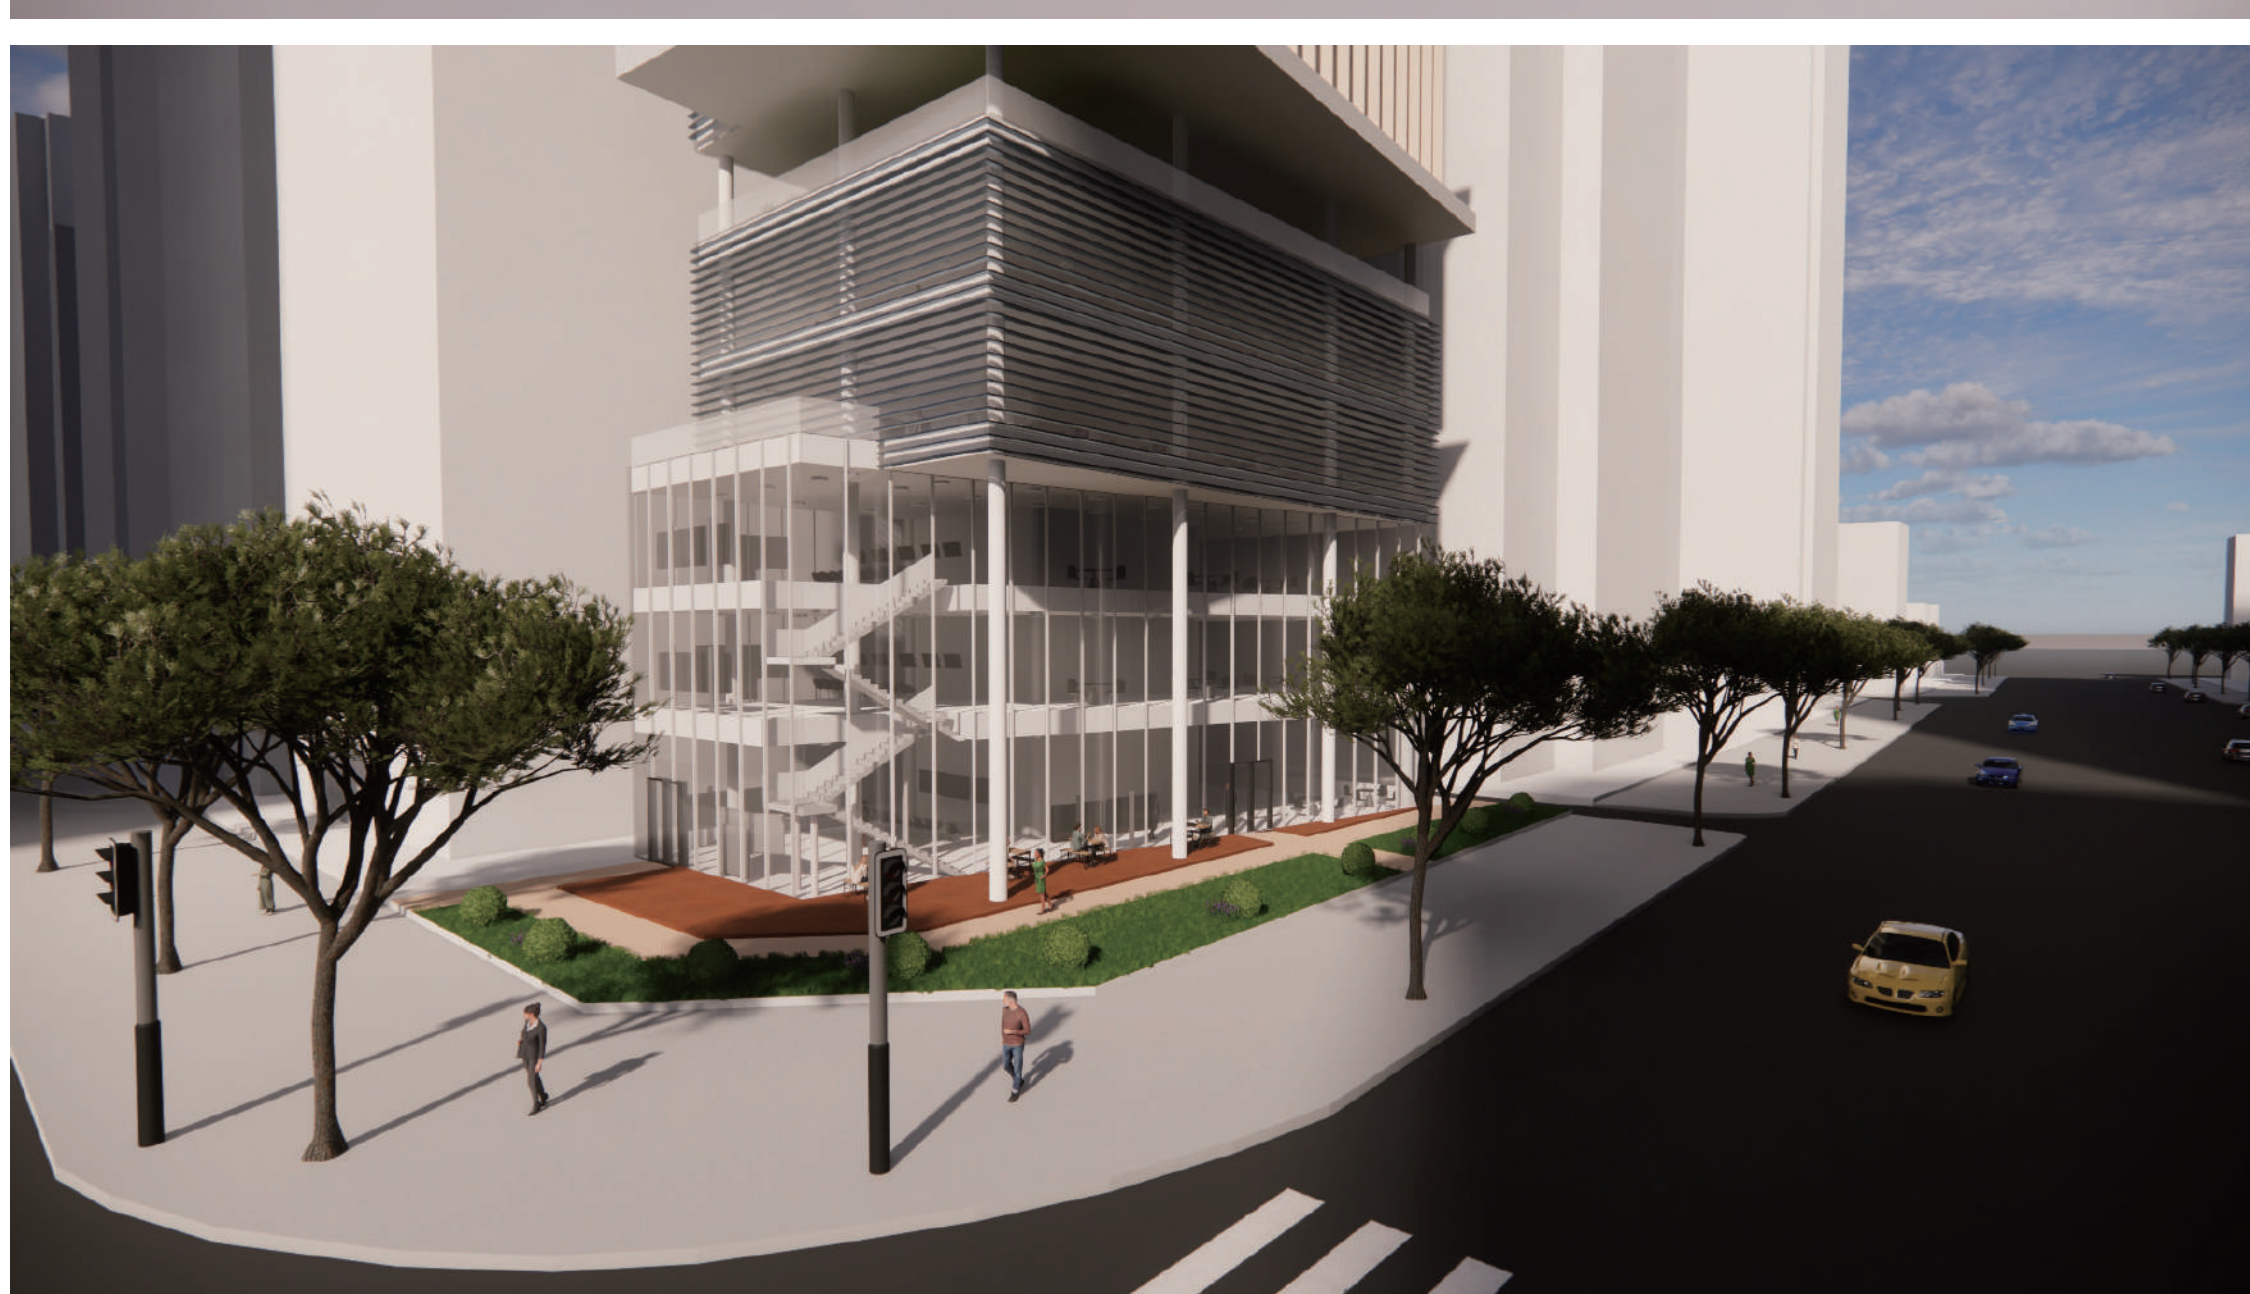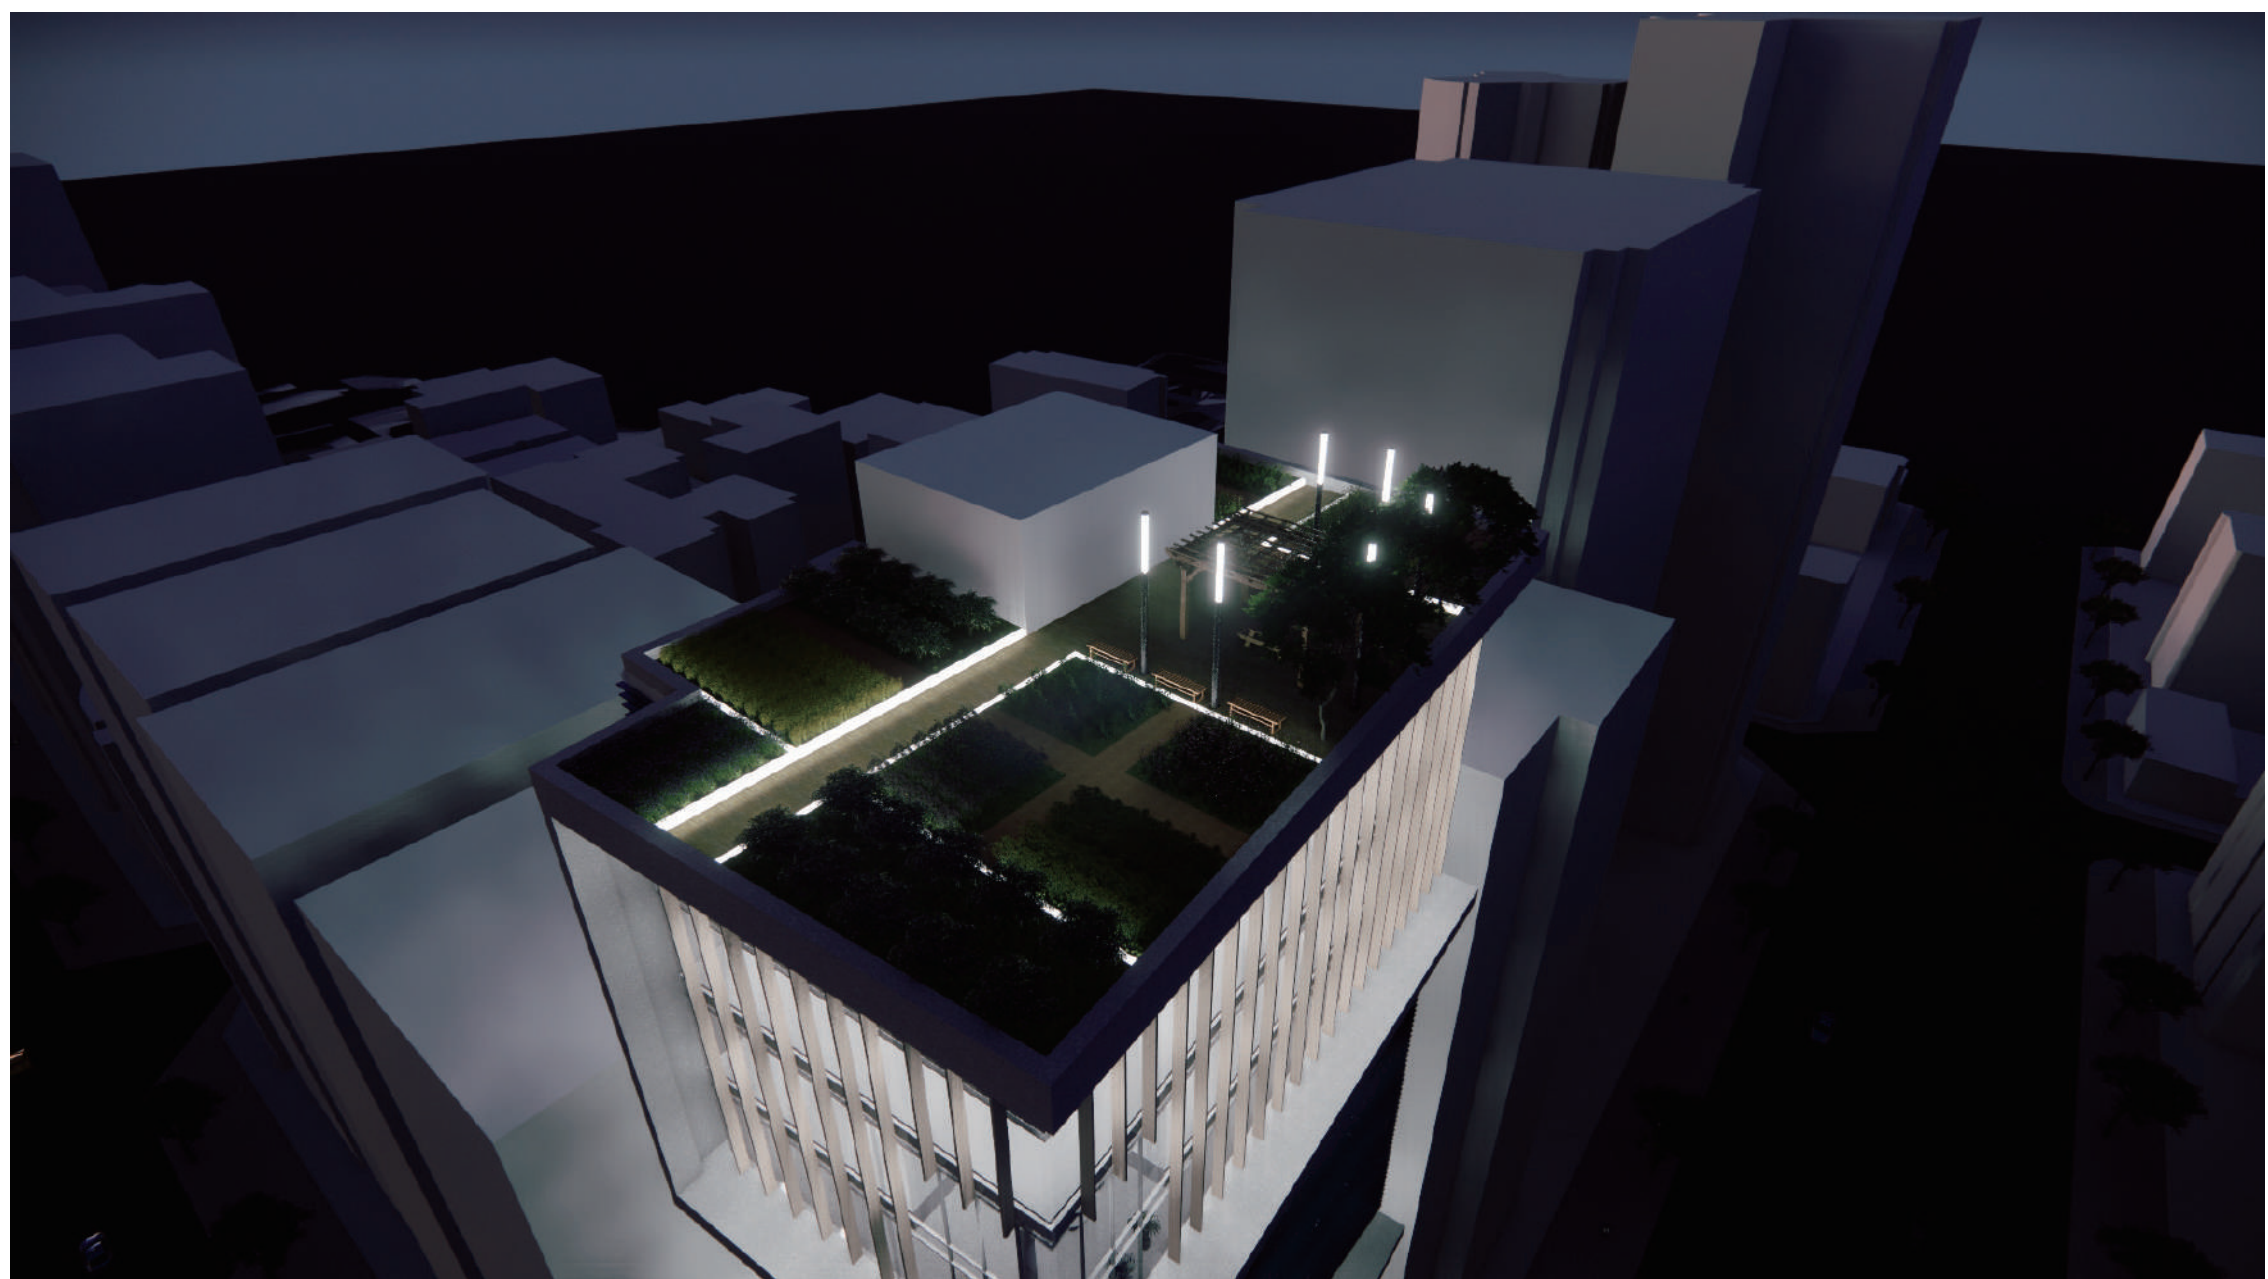


Vertical Section

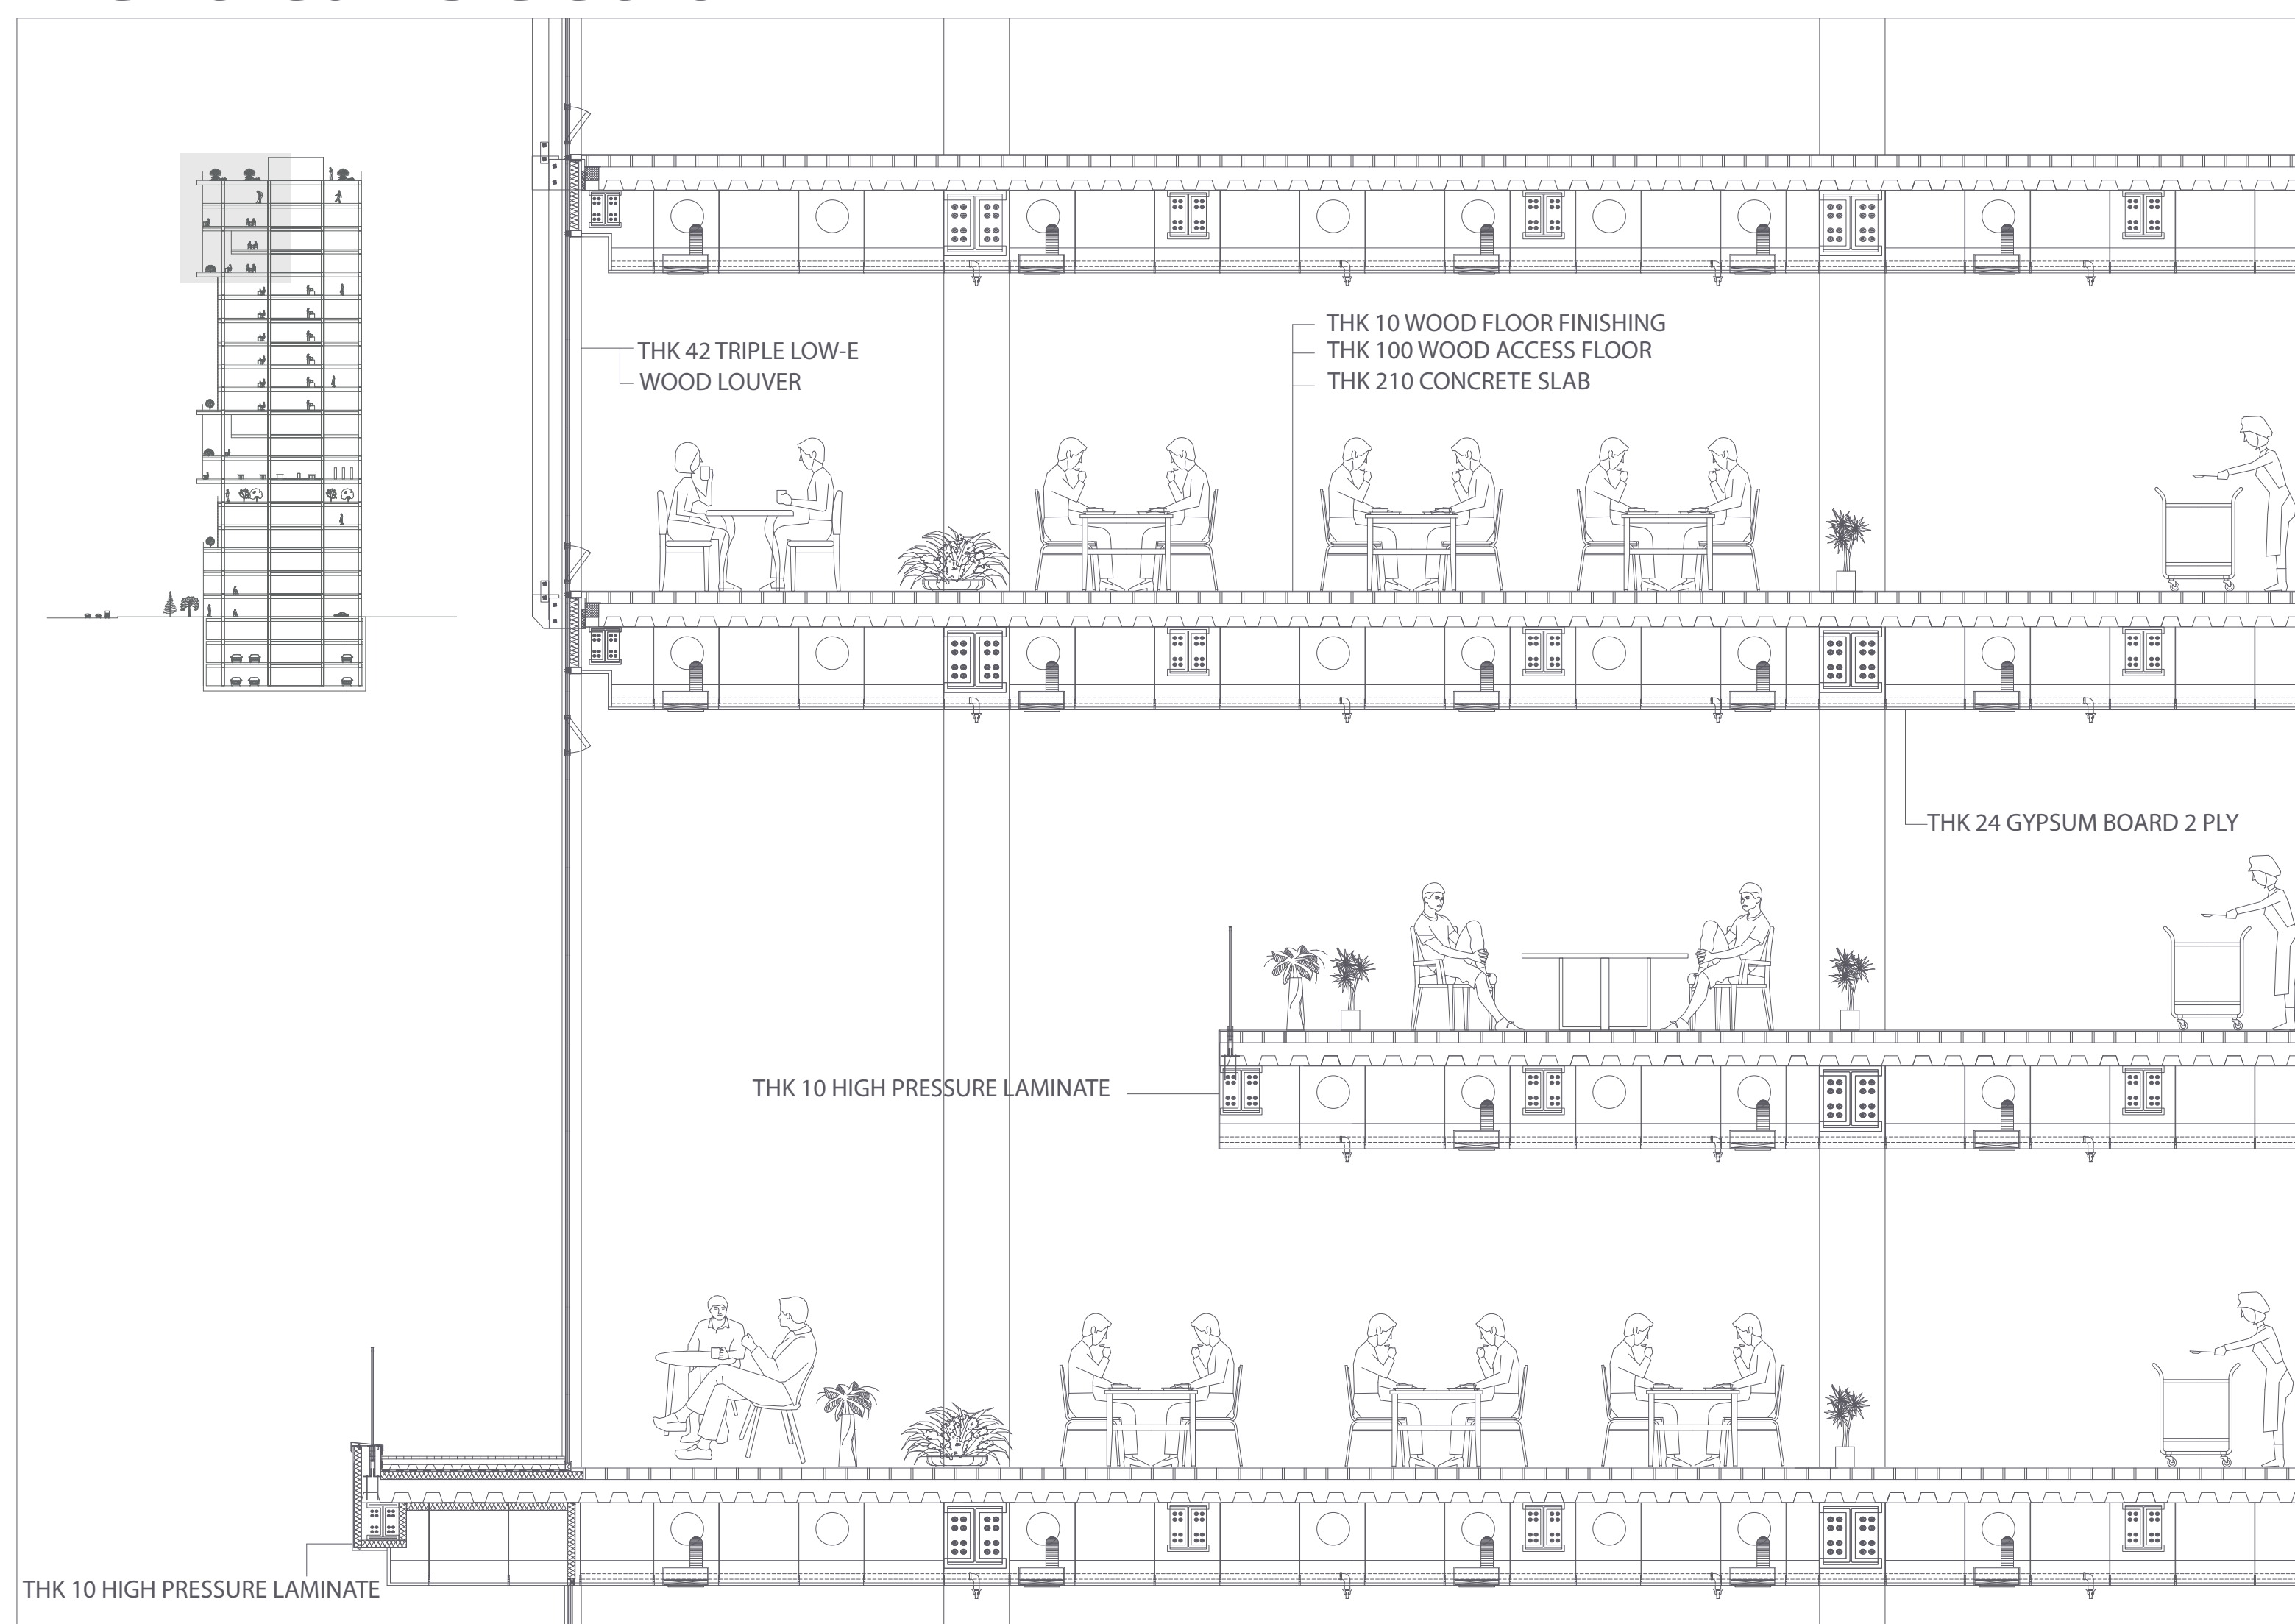


Section Detail

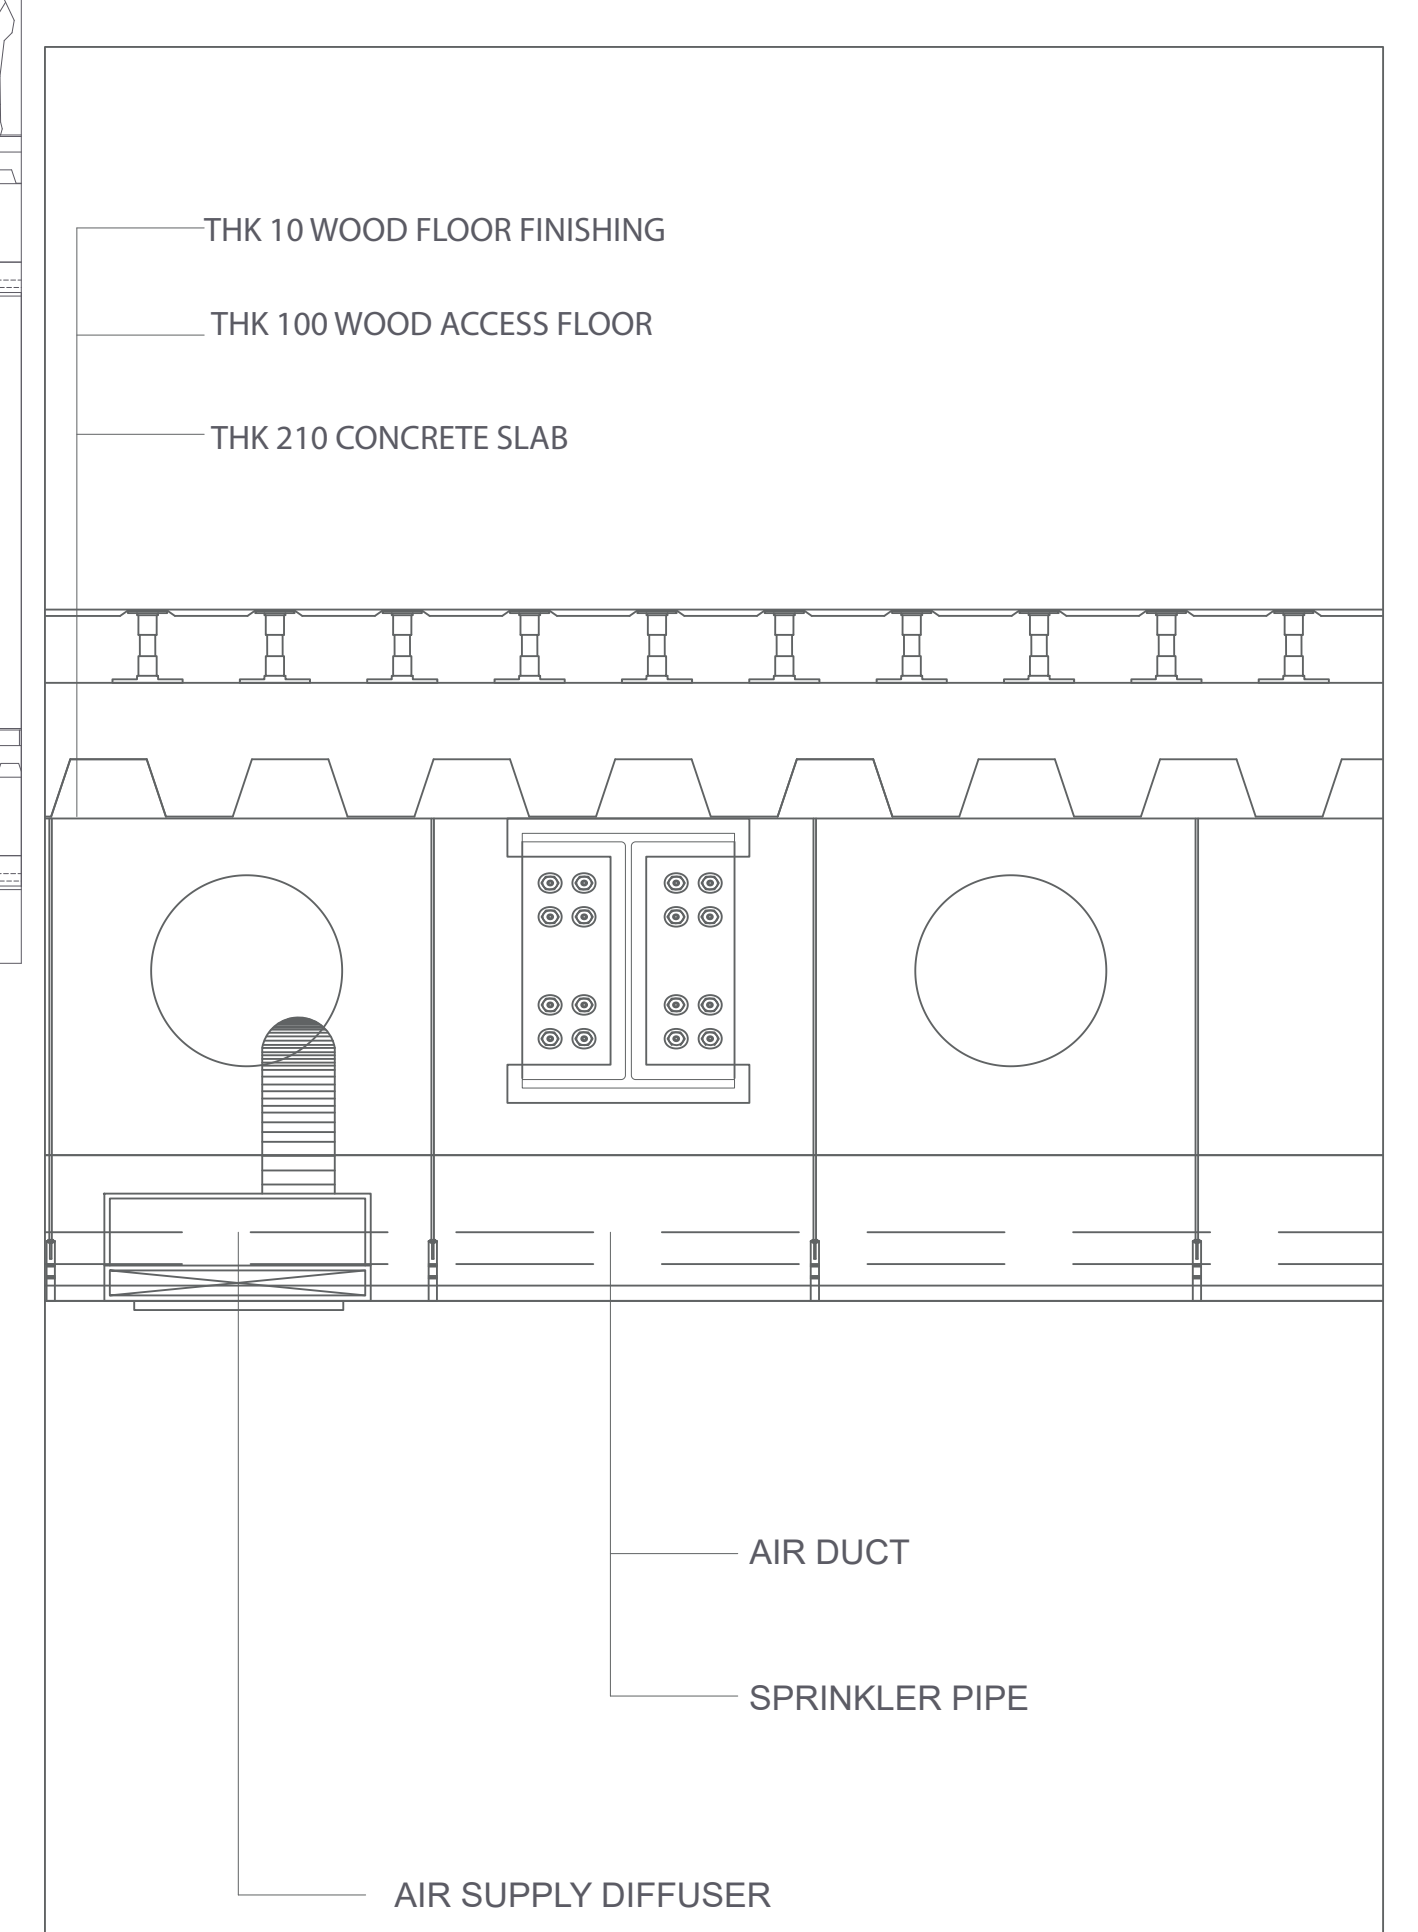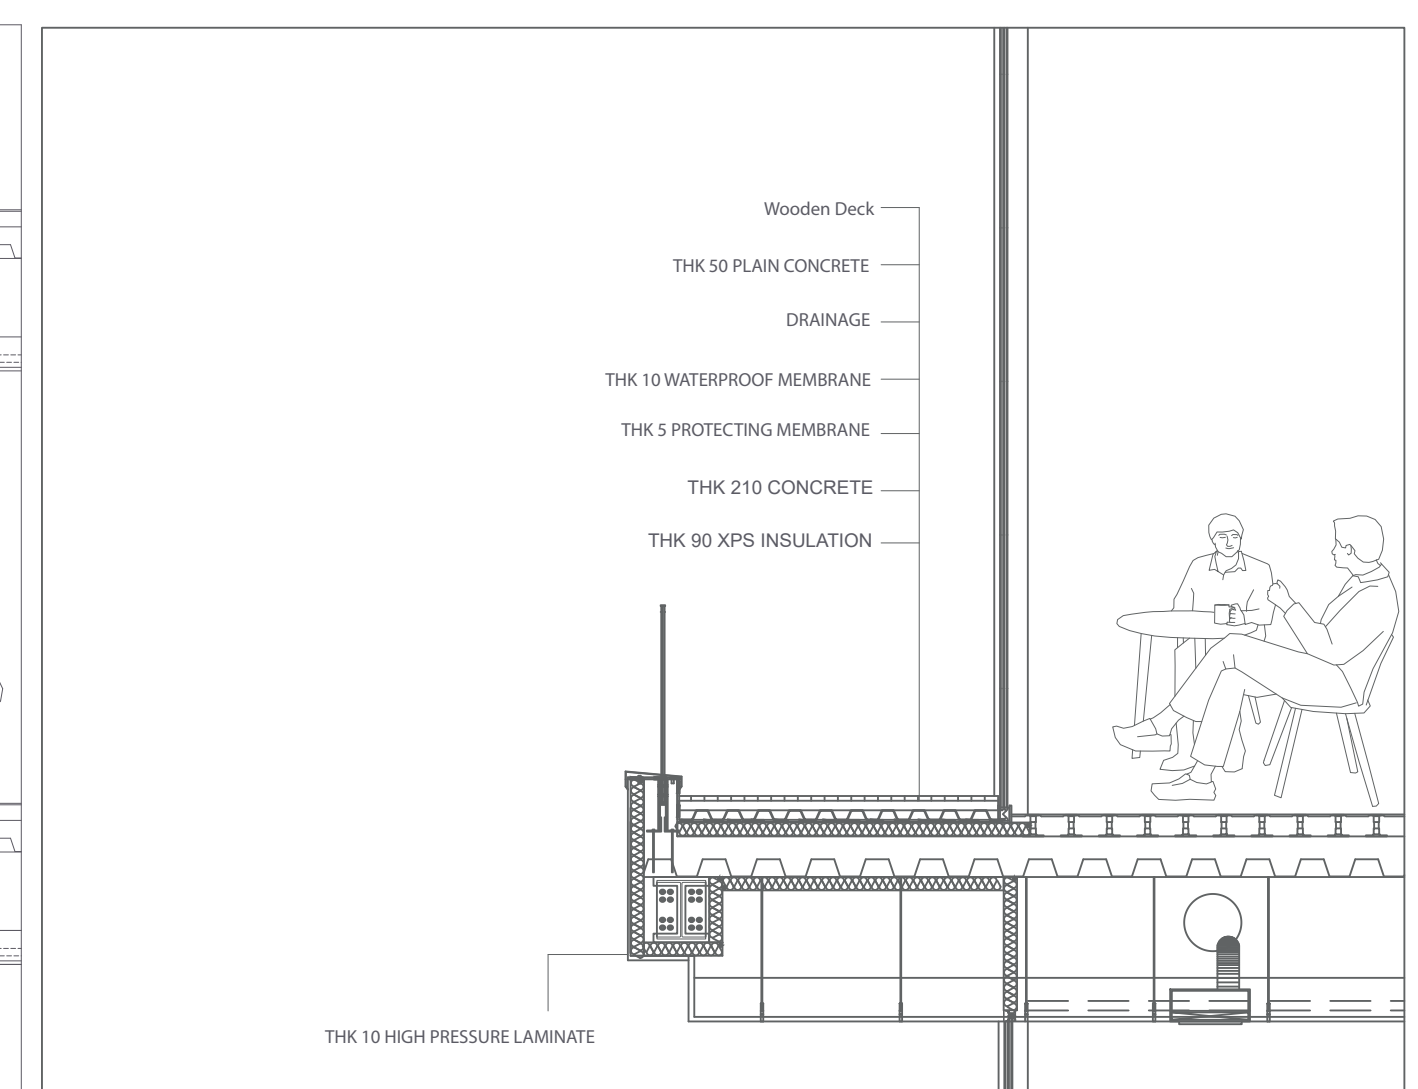

Horizontal Section

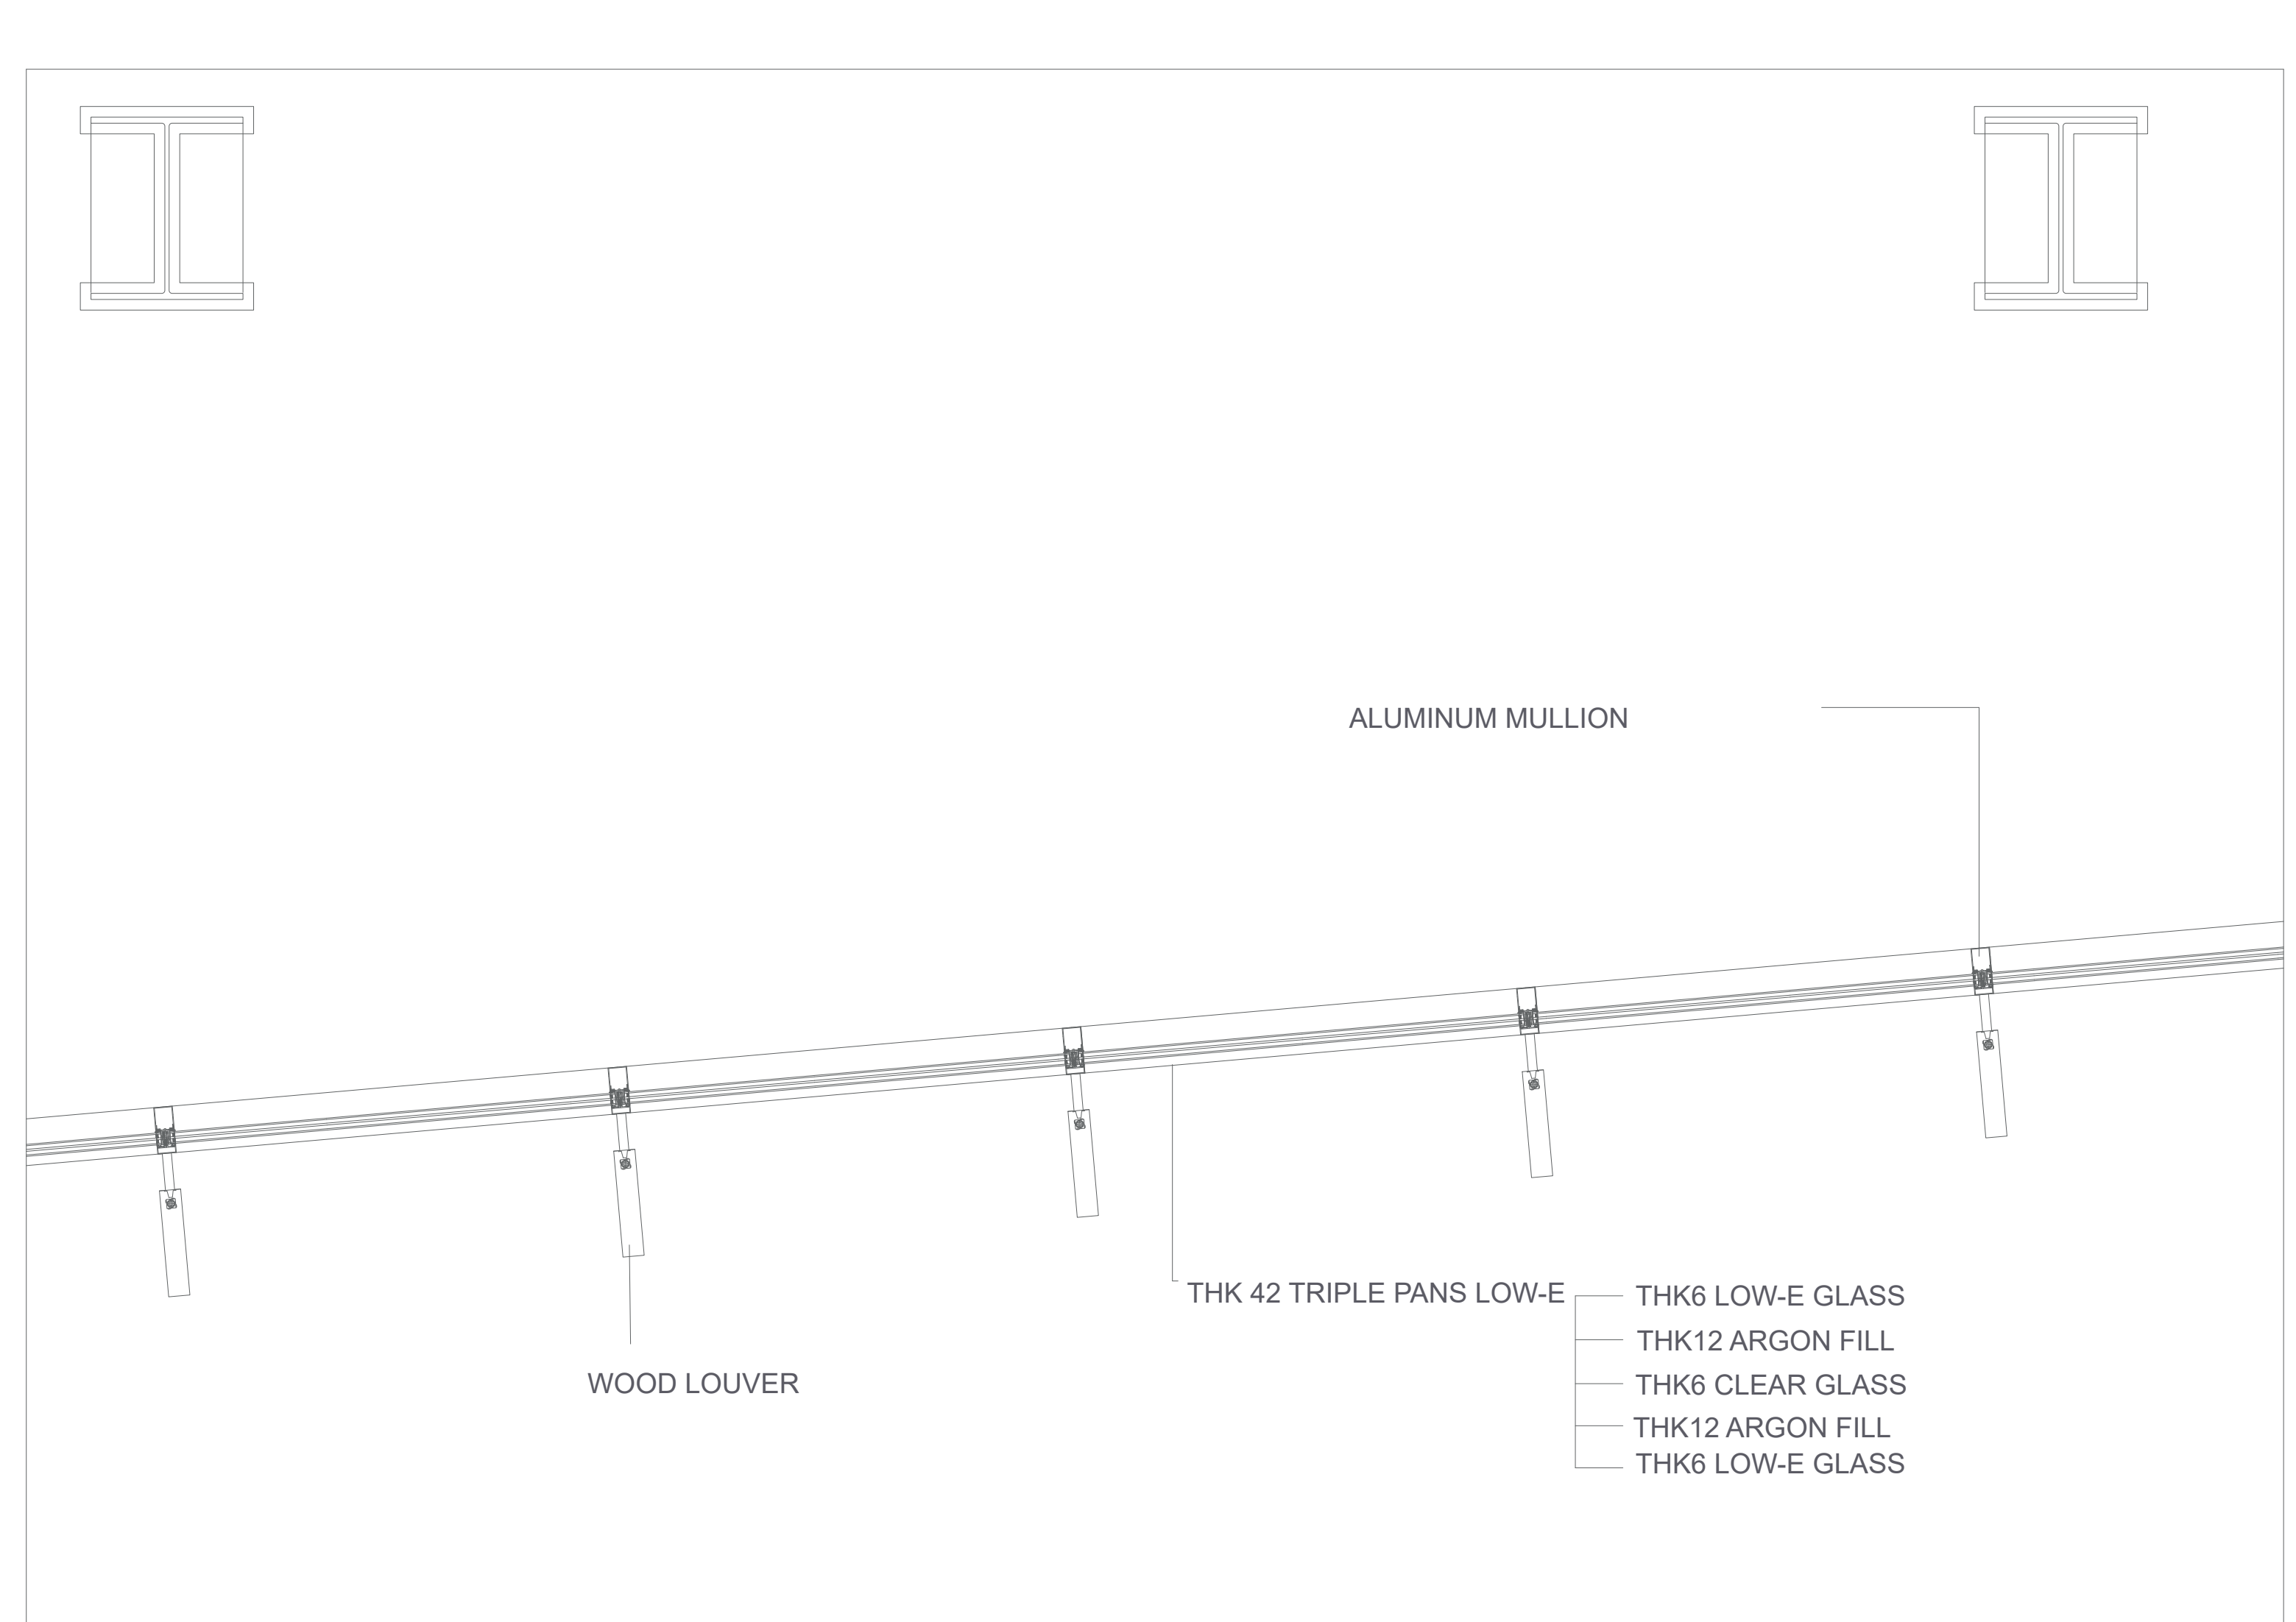


Ventilation

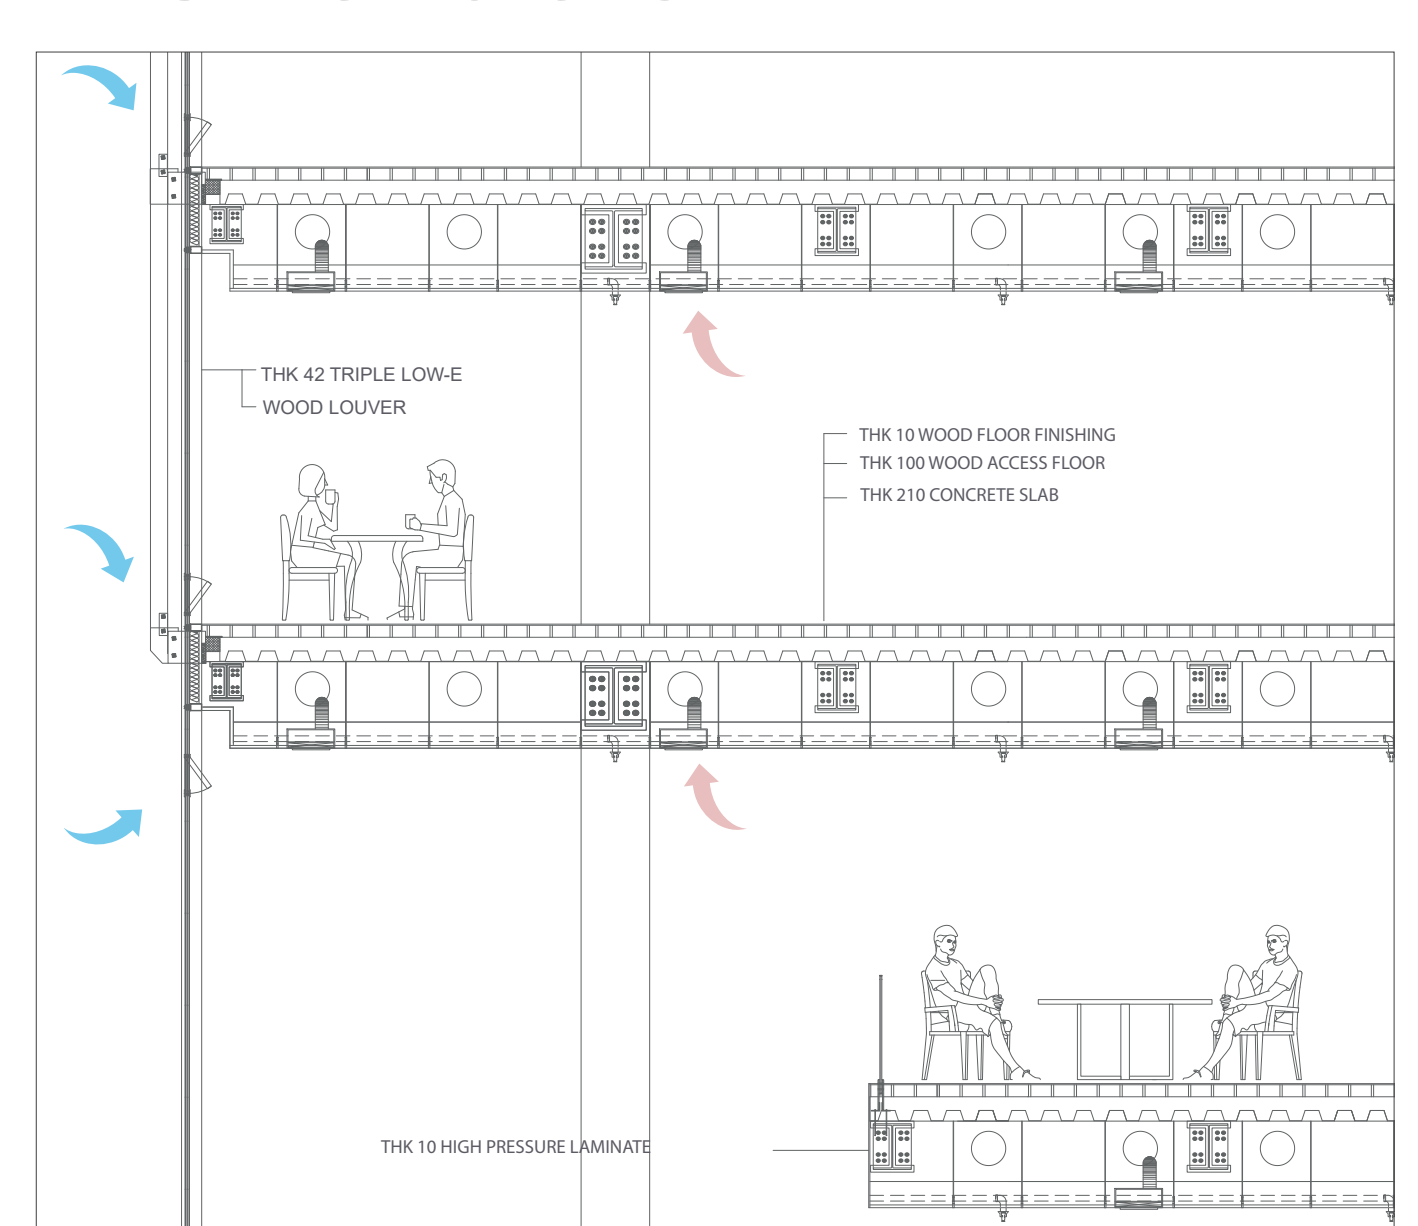

Structure Modeling



Exploded Axonometric

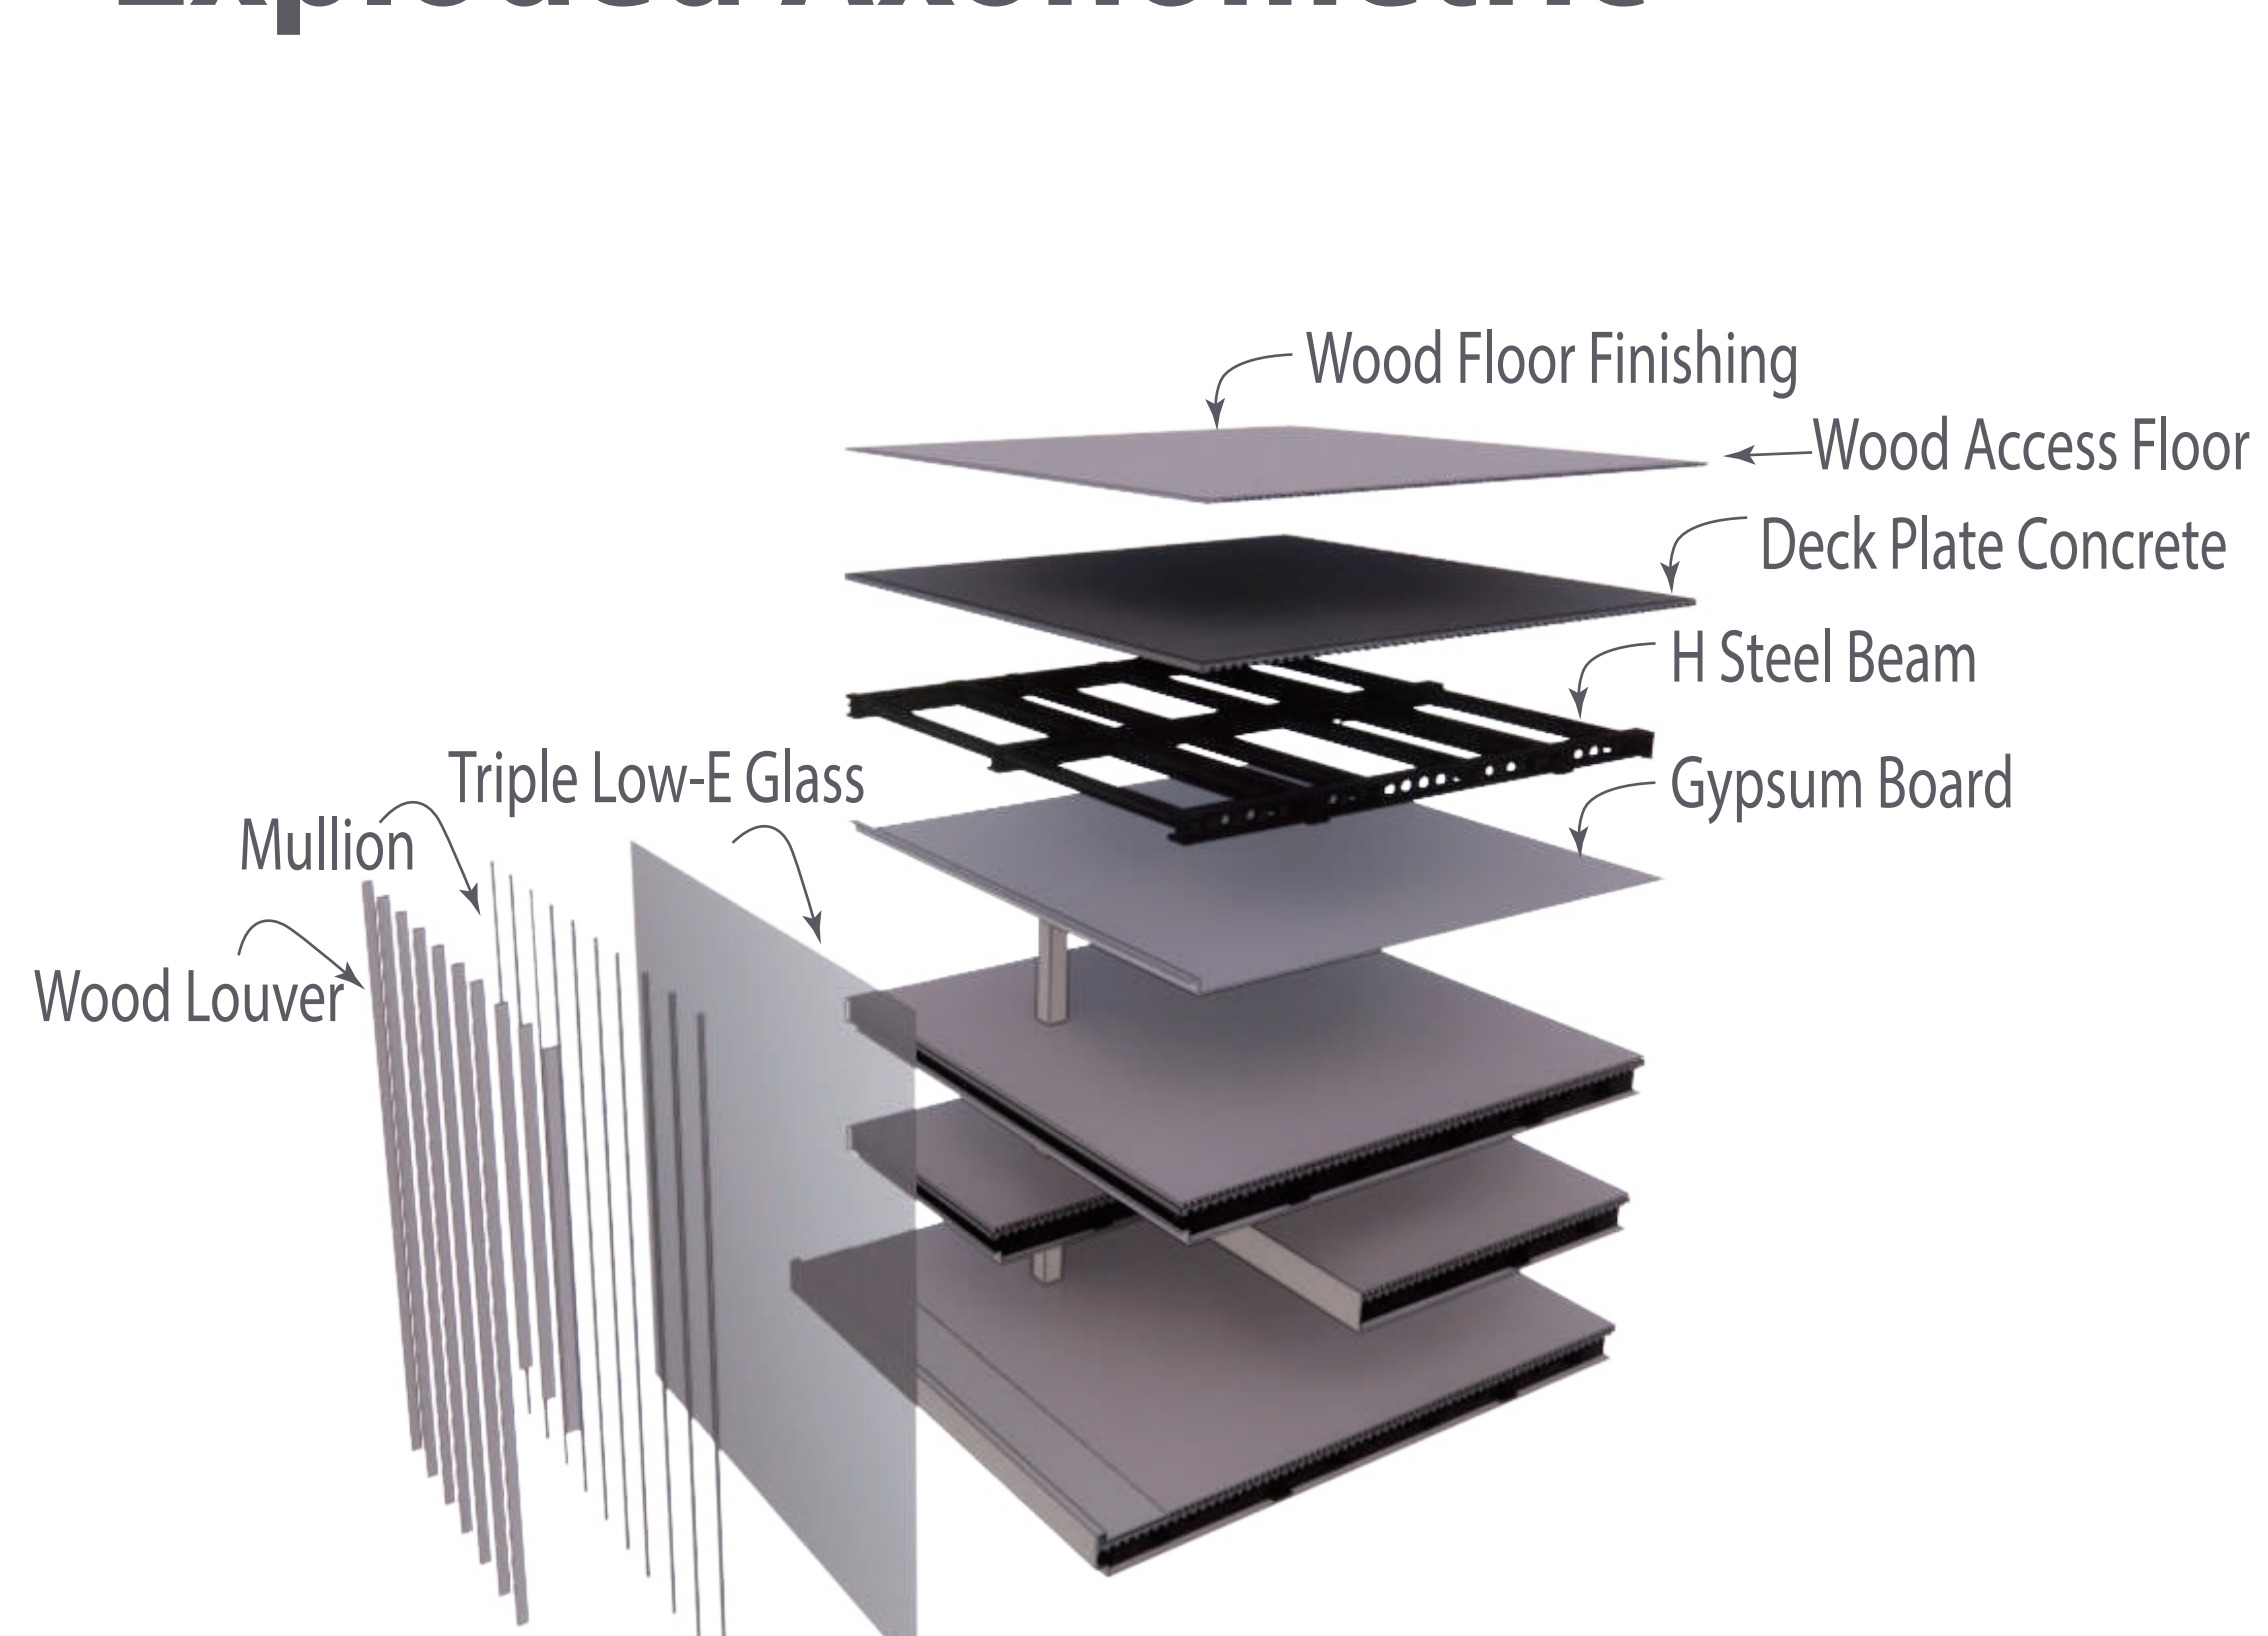

Elevation

